פרט ראש כלונס 2Φ80 340/100/130
פסיעה 3Φ
קנ"מ 1:25

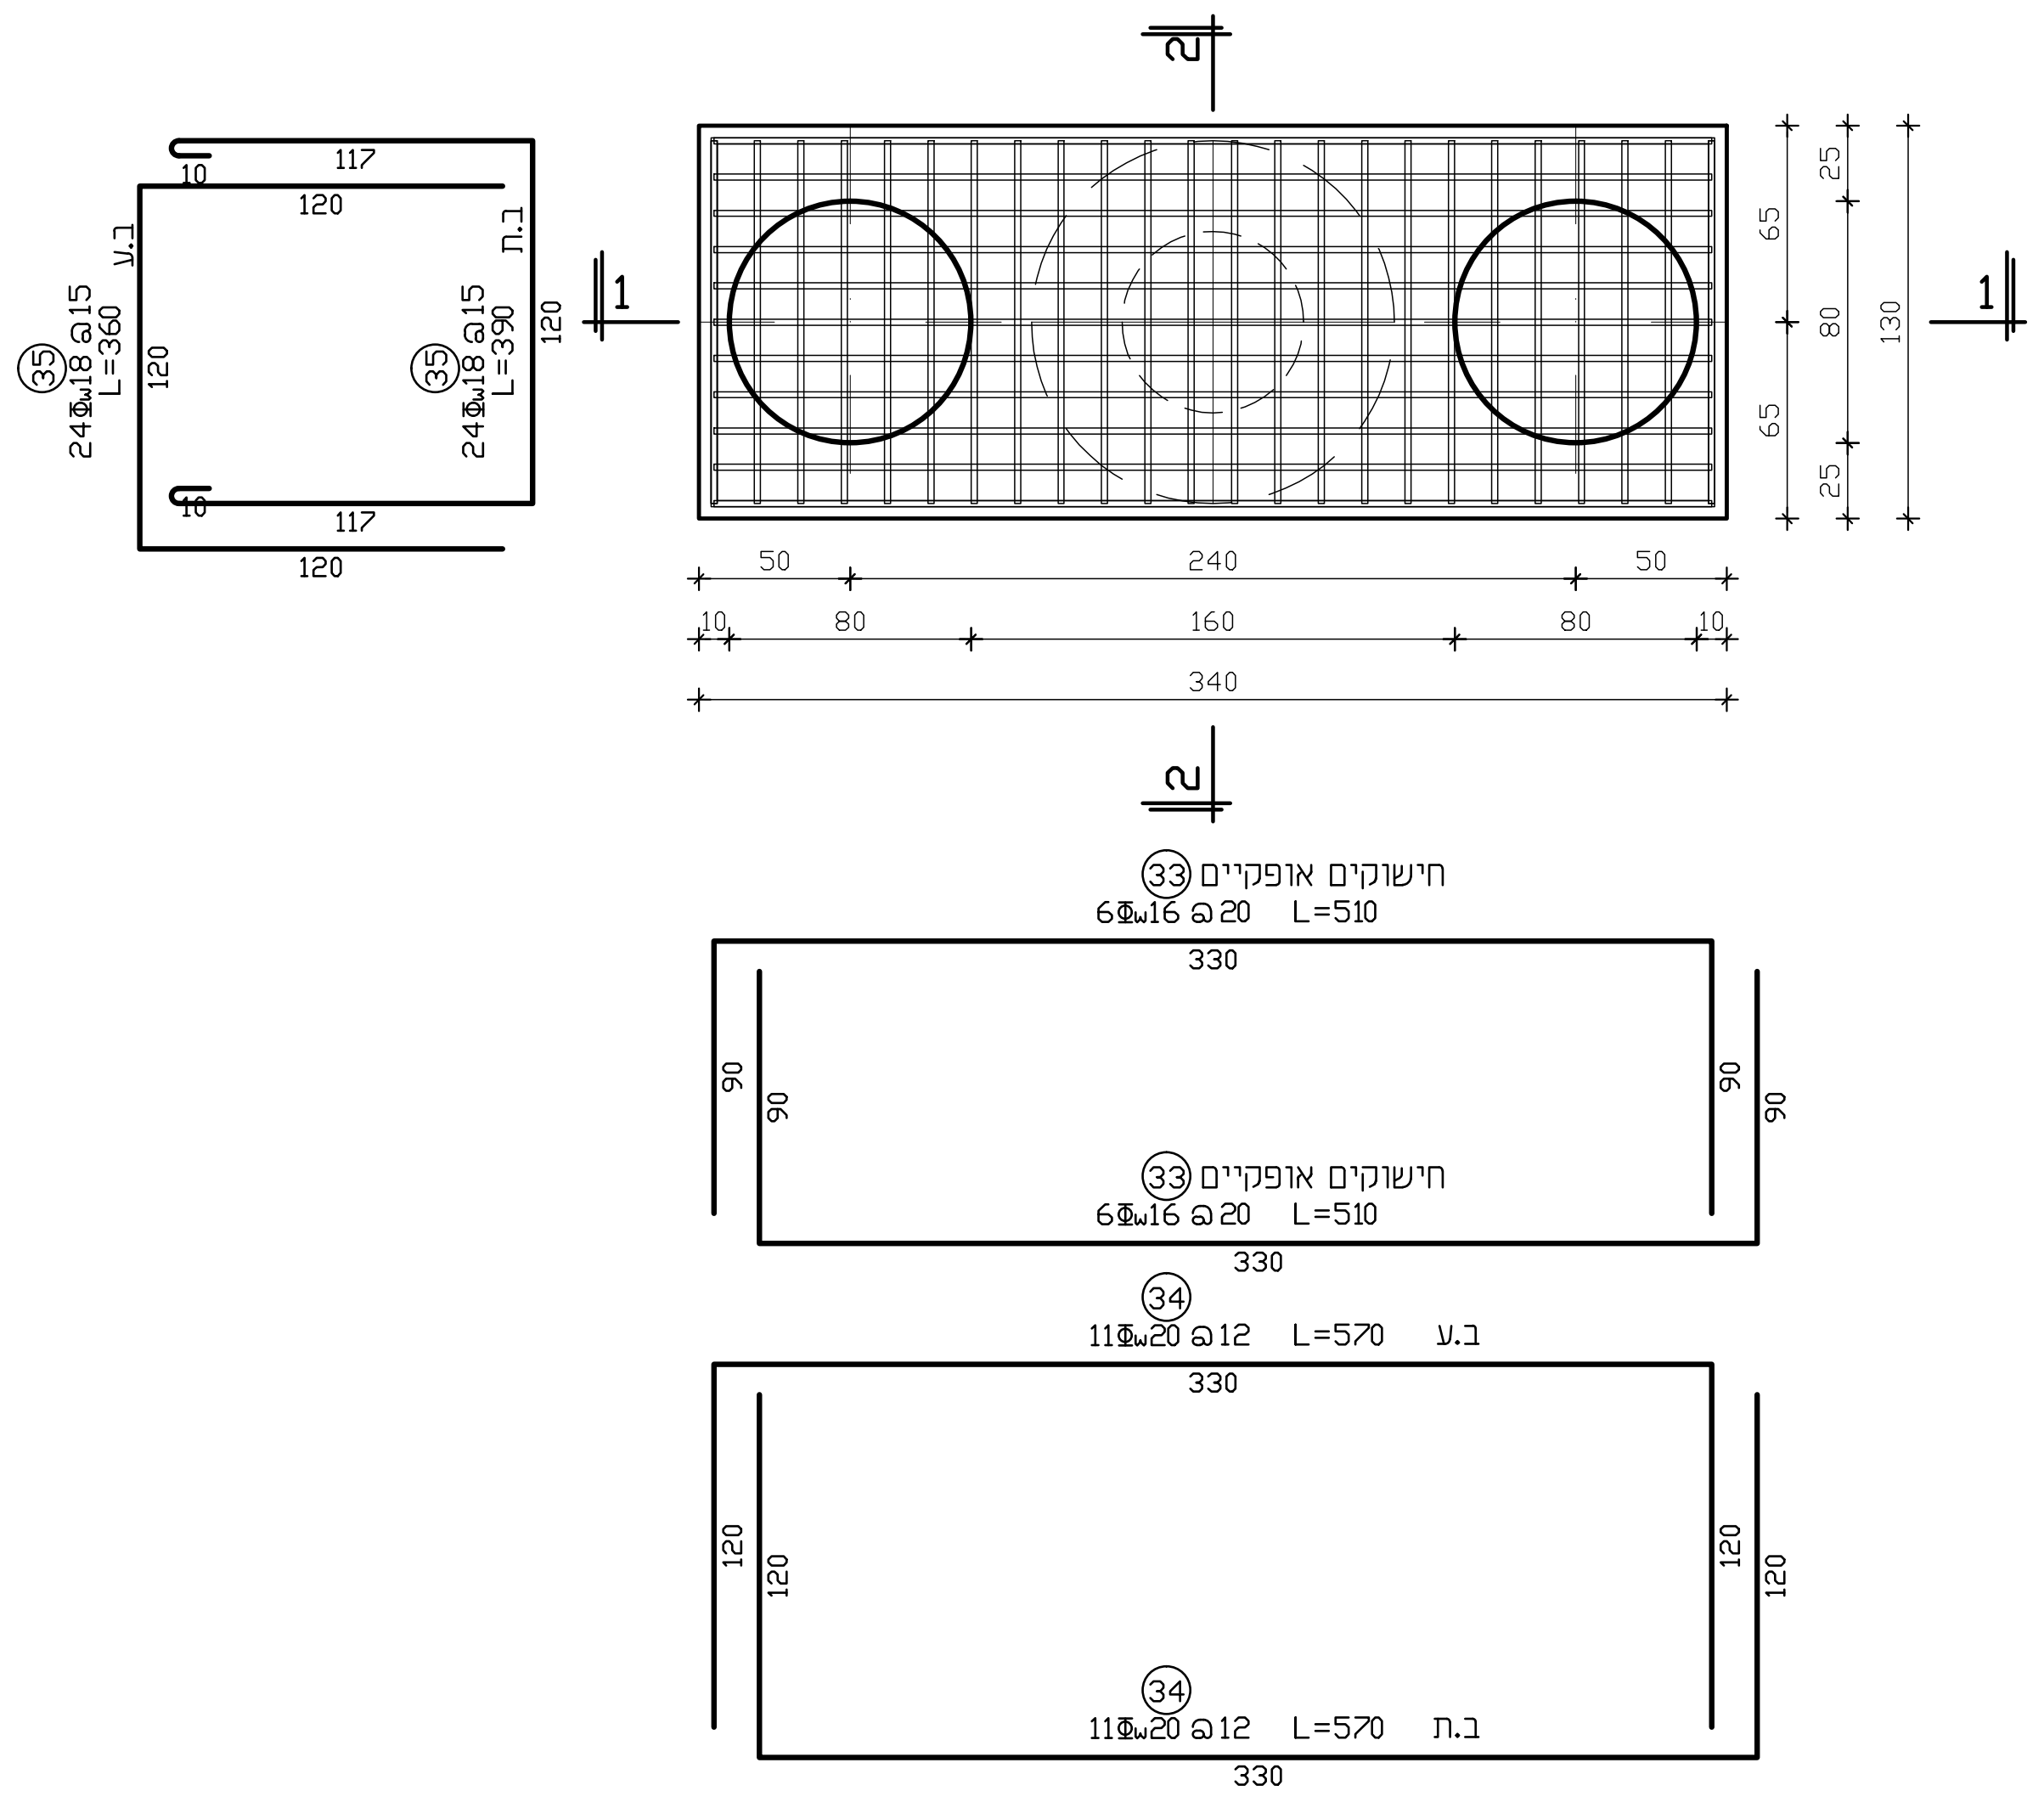

חתך 1-1
קנ"מ 1:25

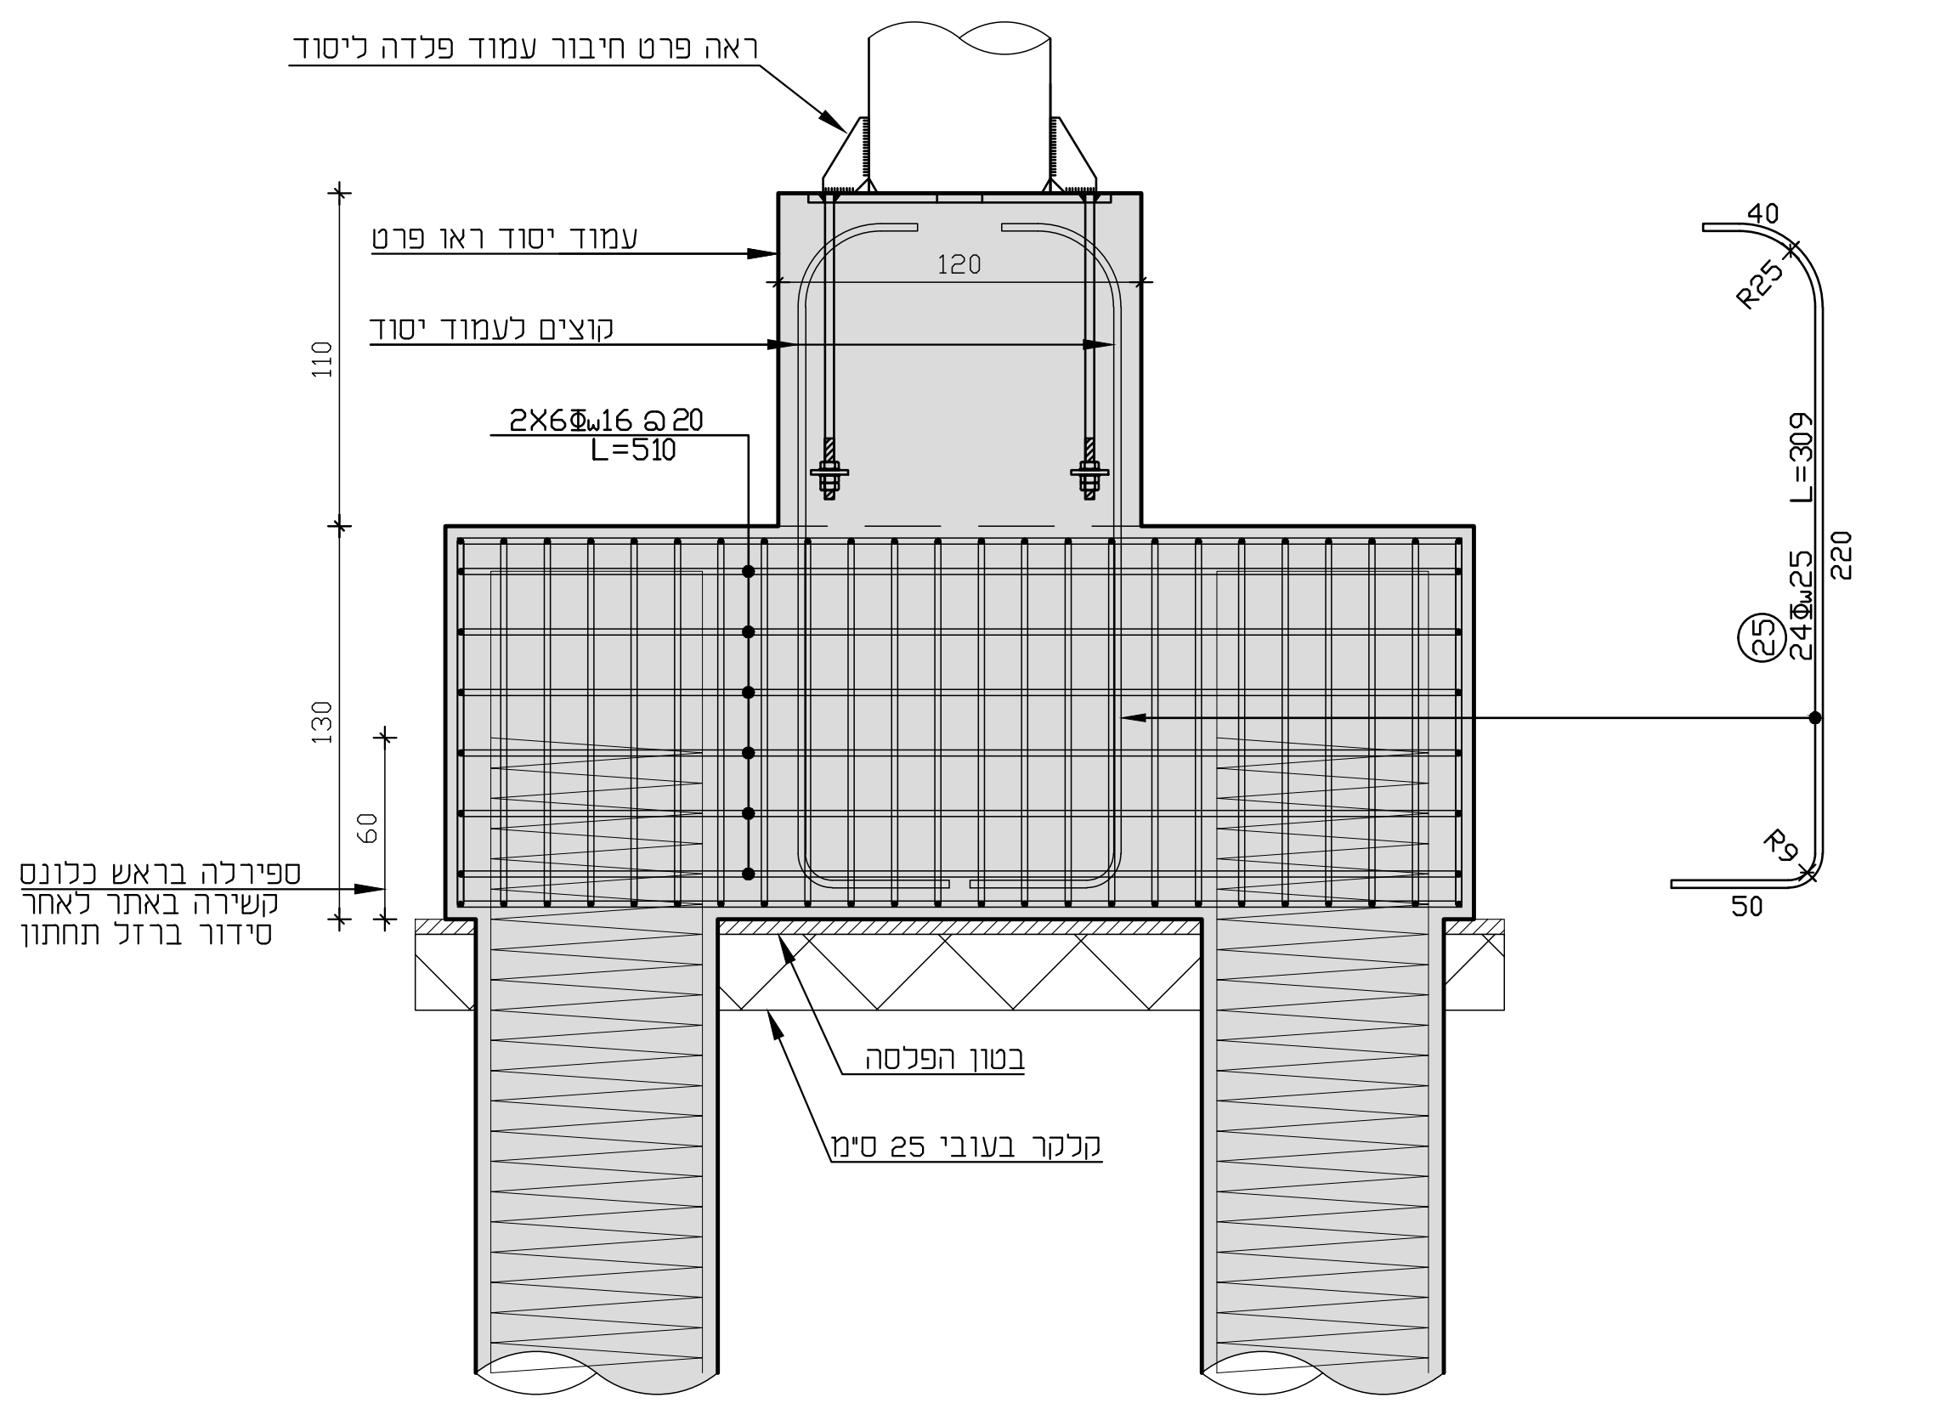

חתך 2-2
קנ"מ 1:25

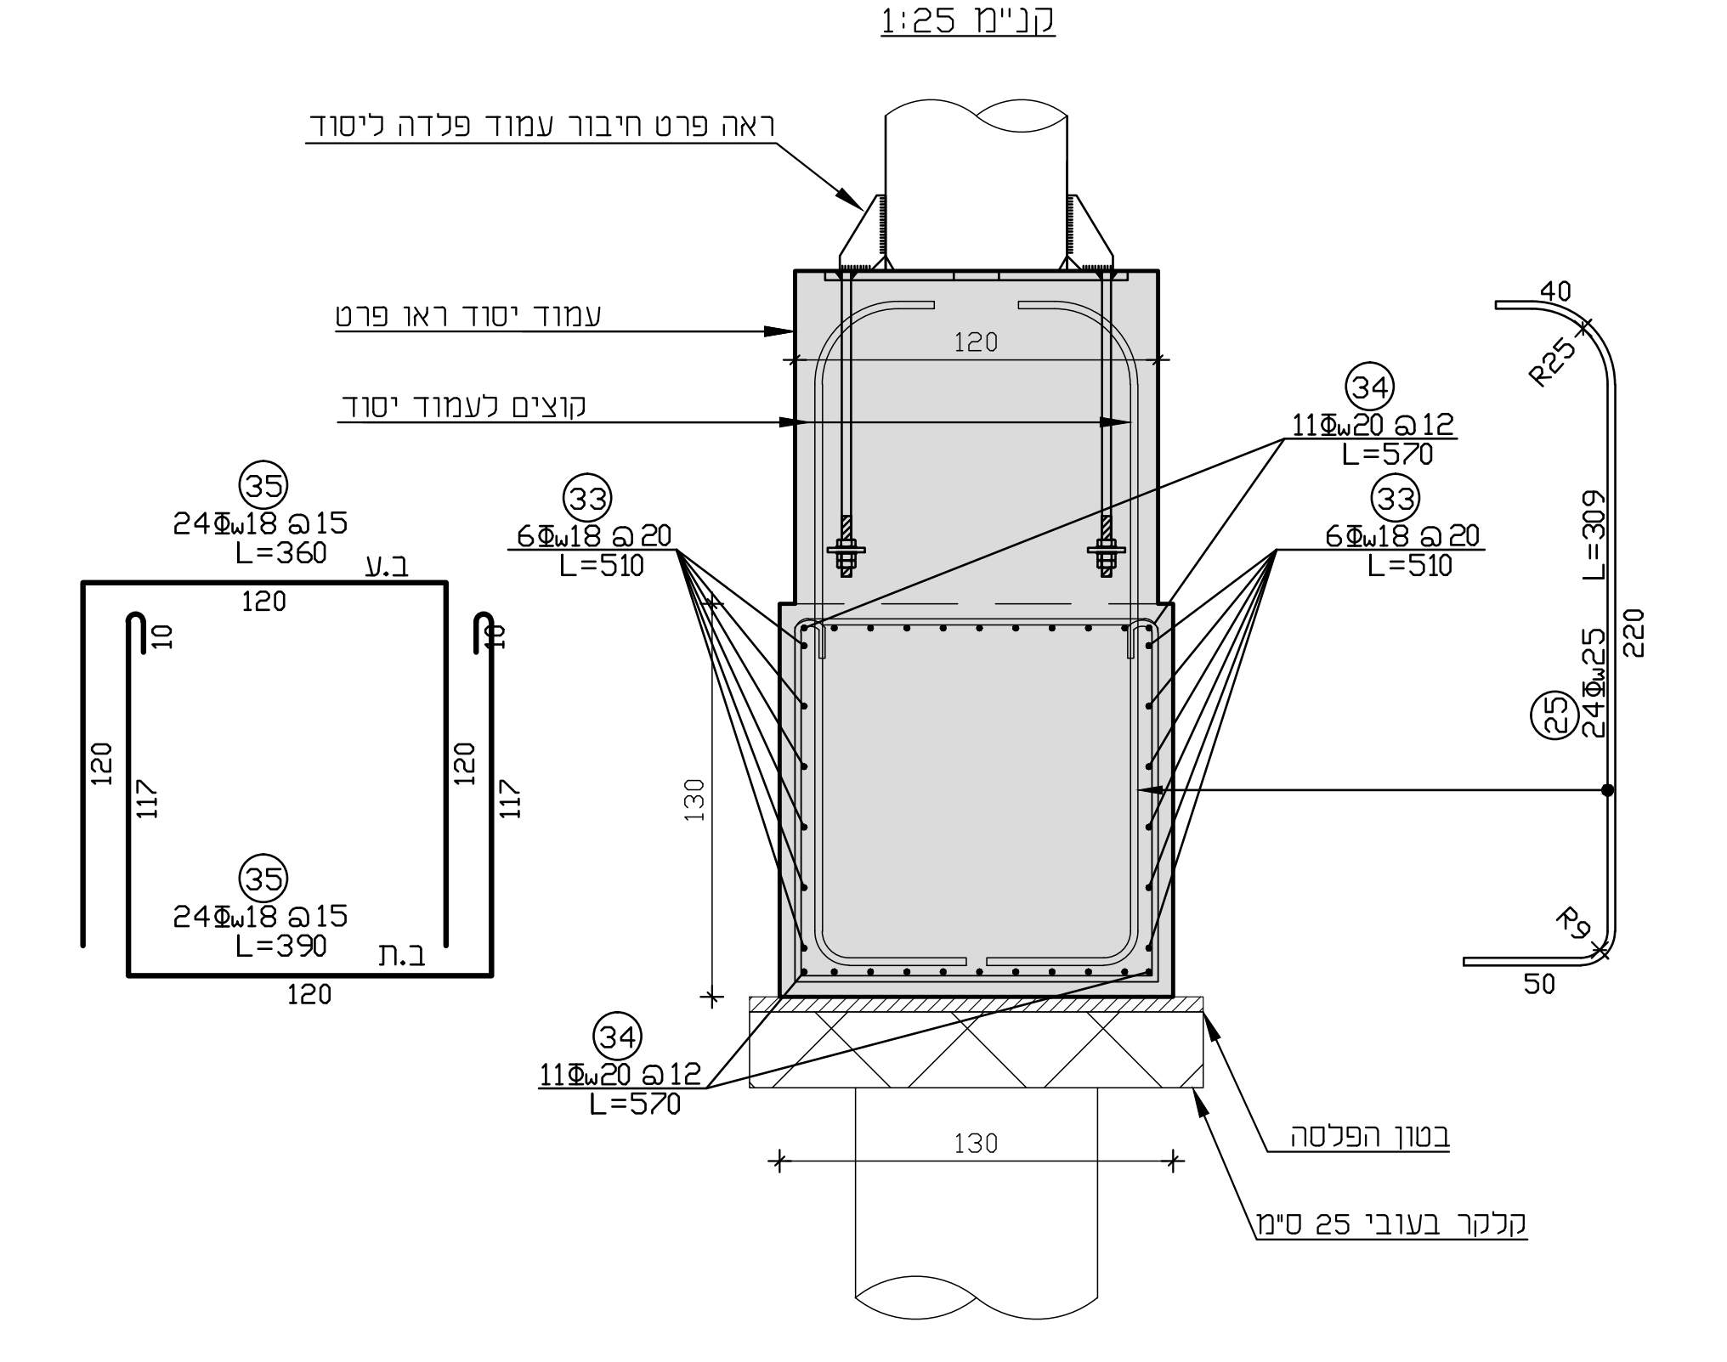

פרט ראשי כלונסאות 3Φ80 H=130
פסיעה 3Φ
קנ"מ 1:25

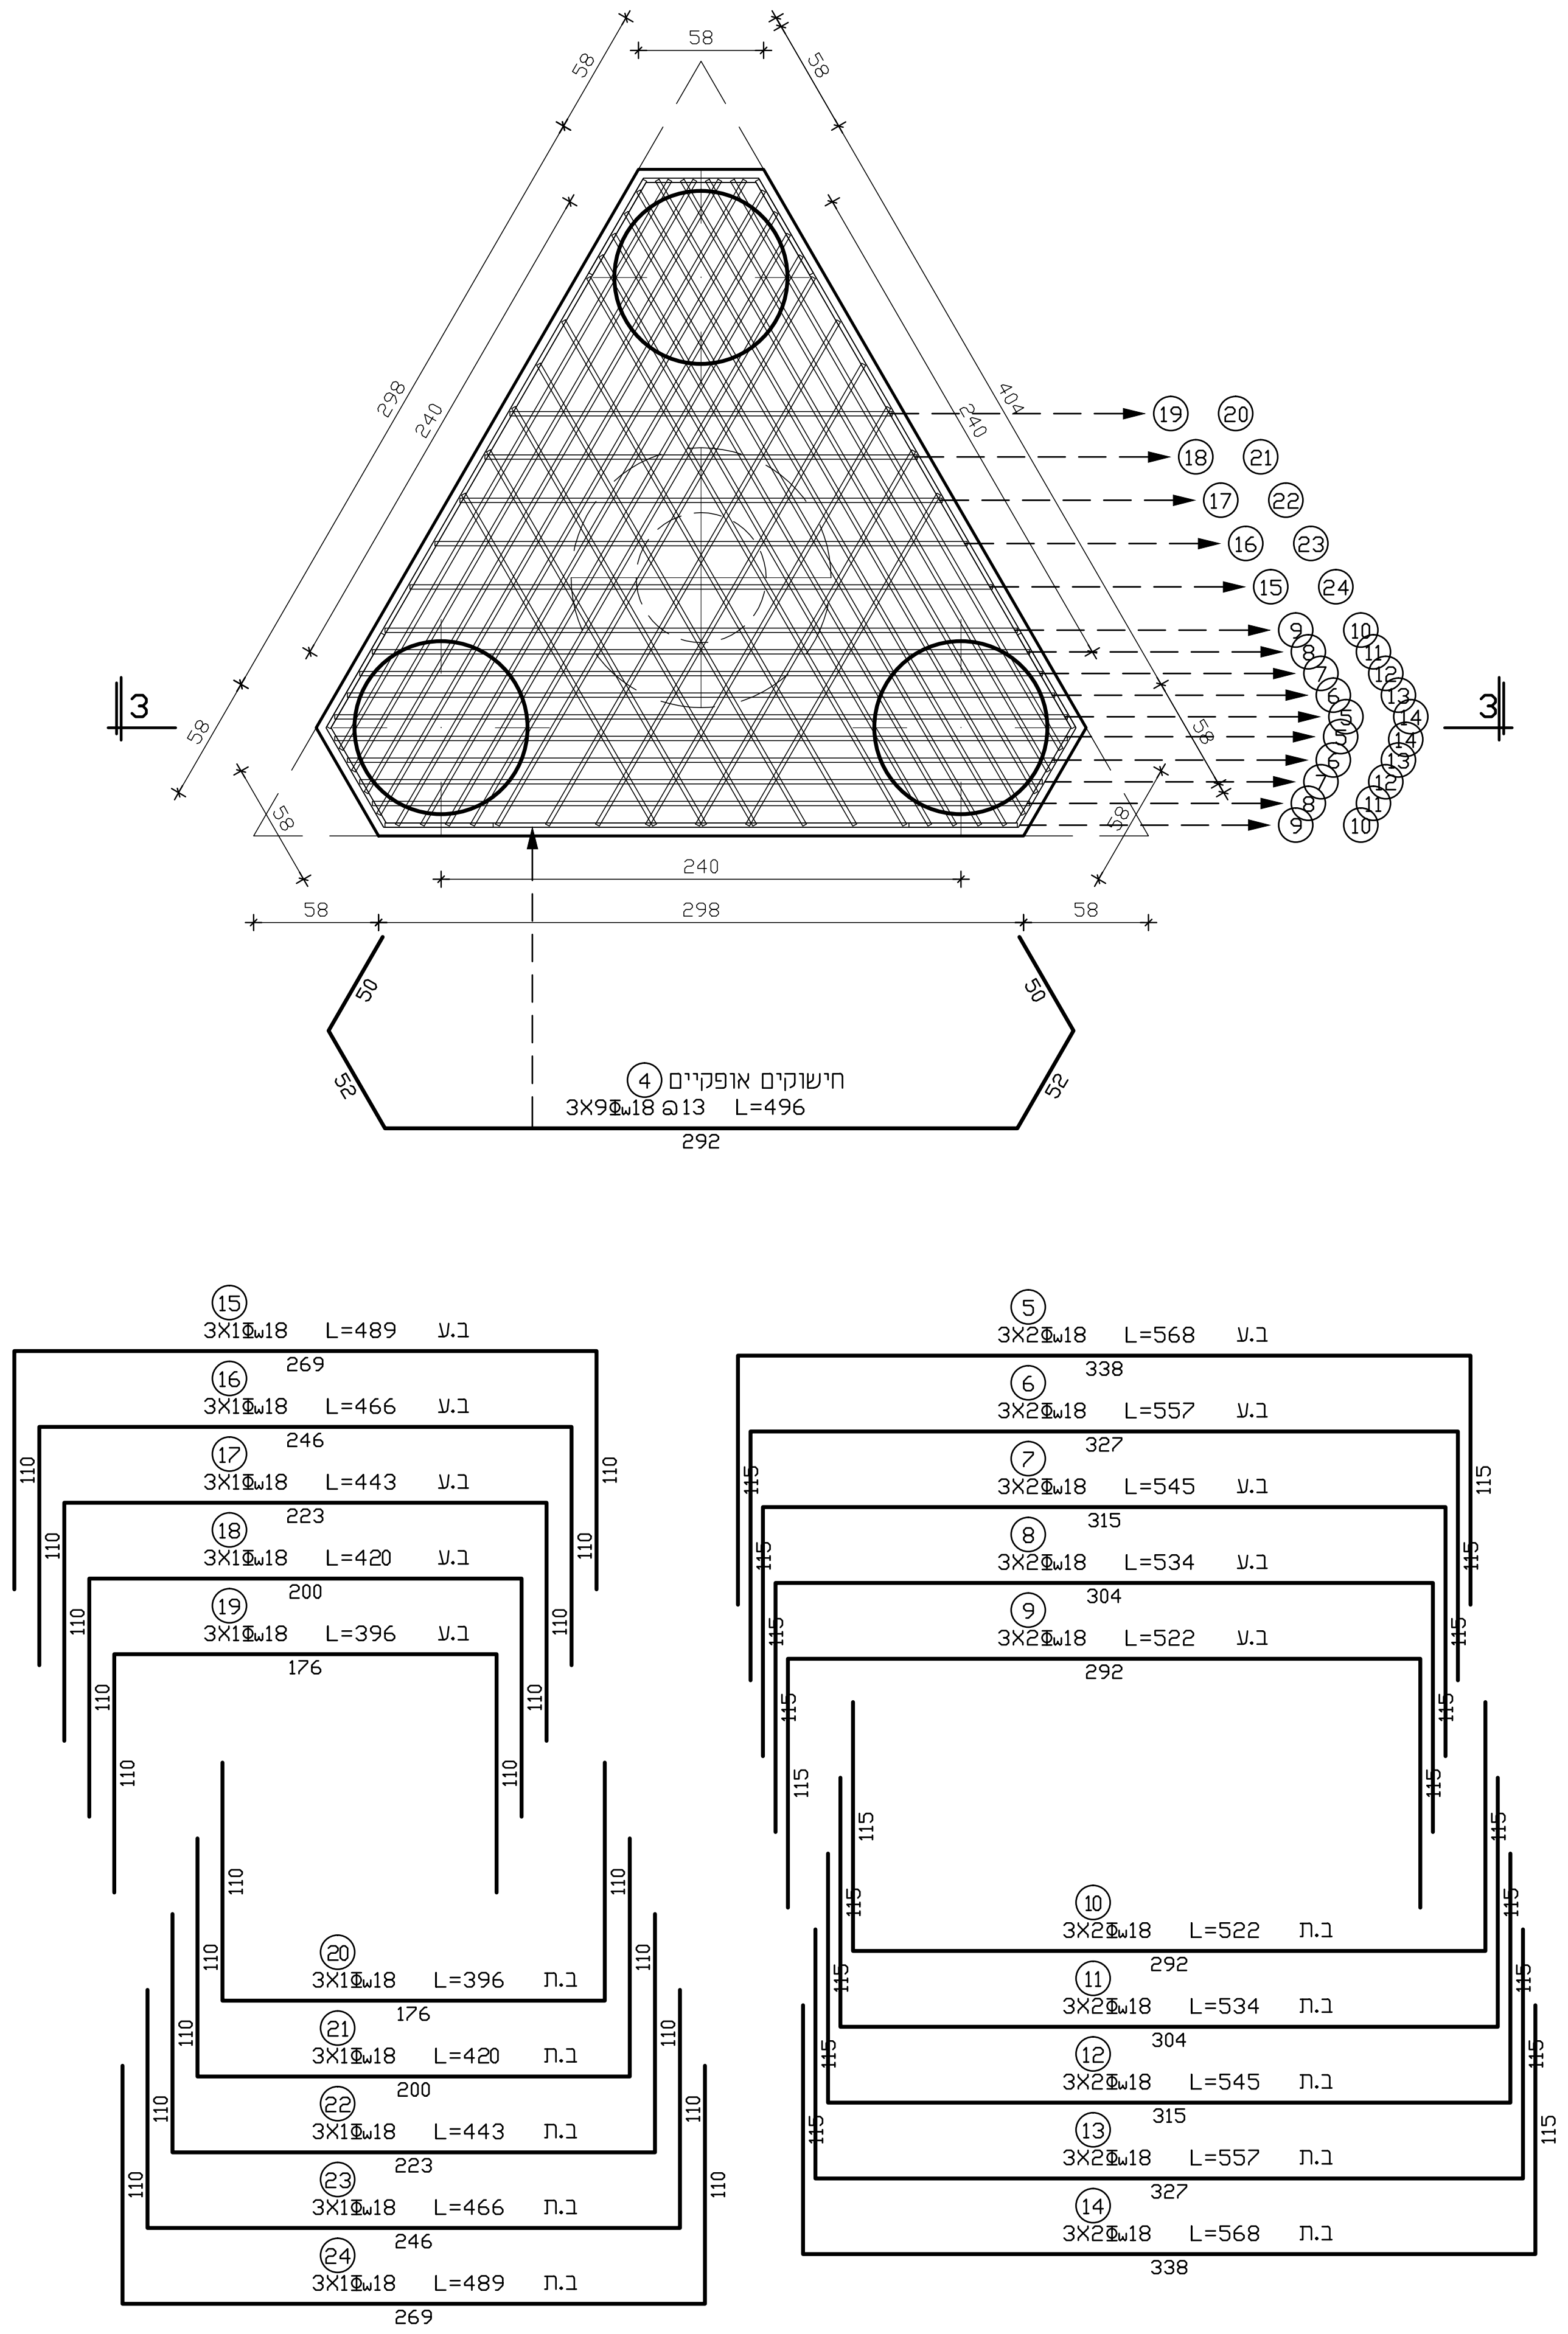

חתך 3-3
קנ"מ 1:25

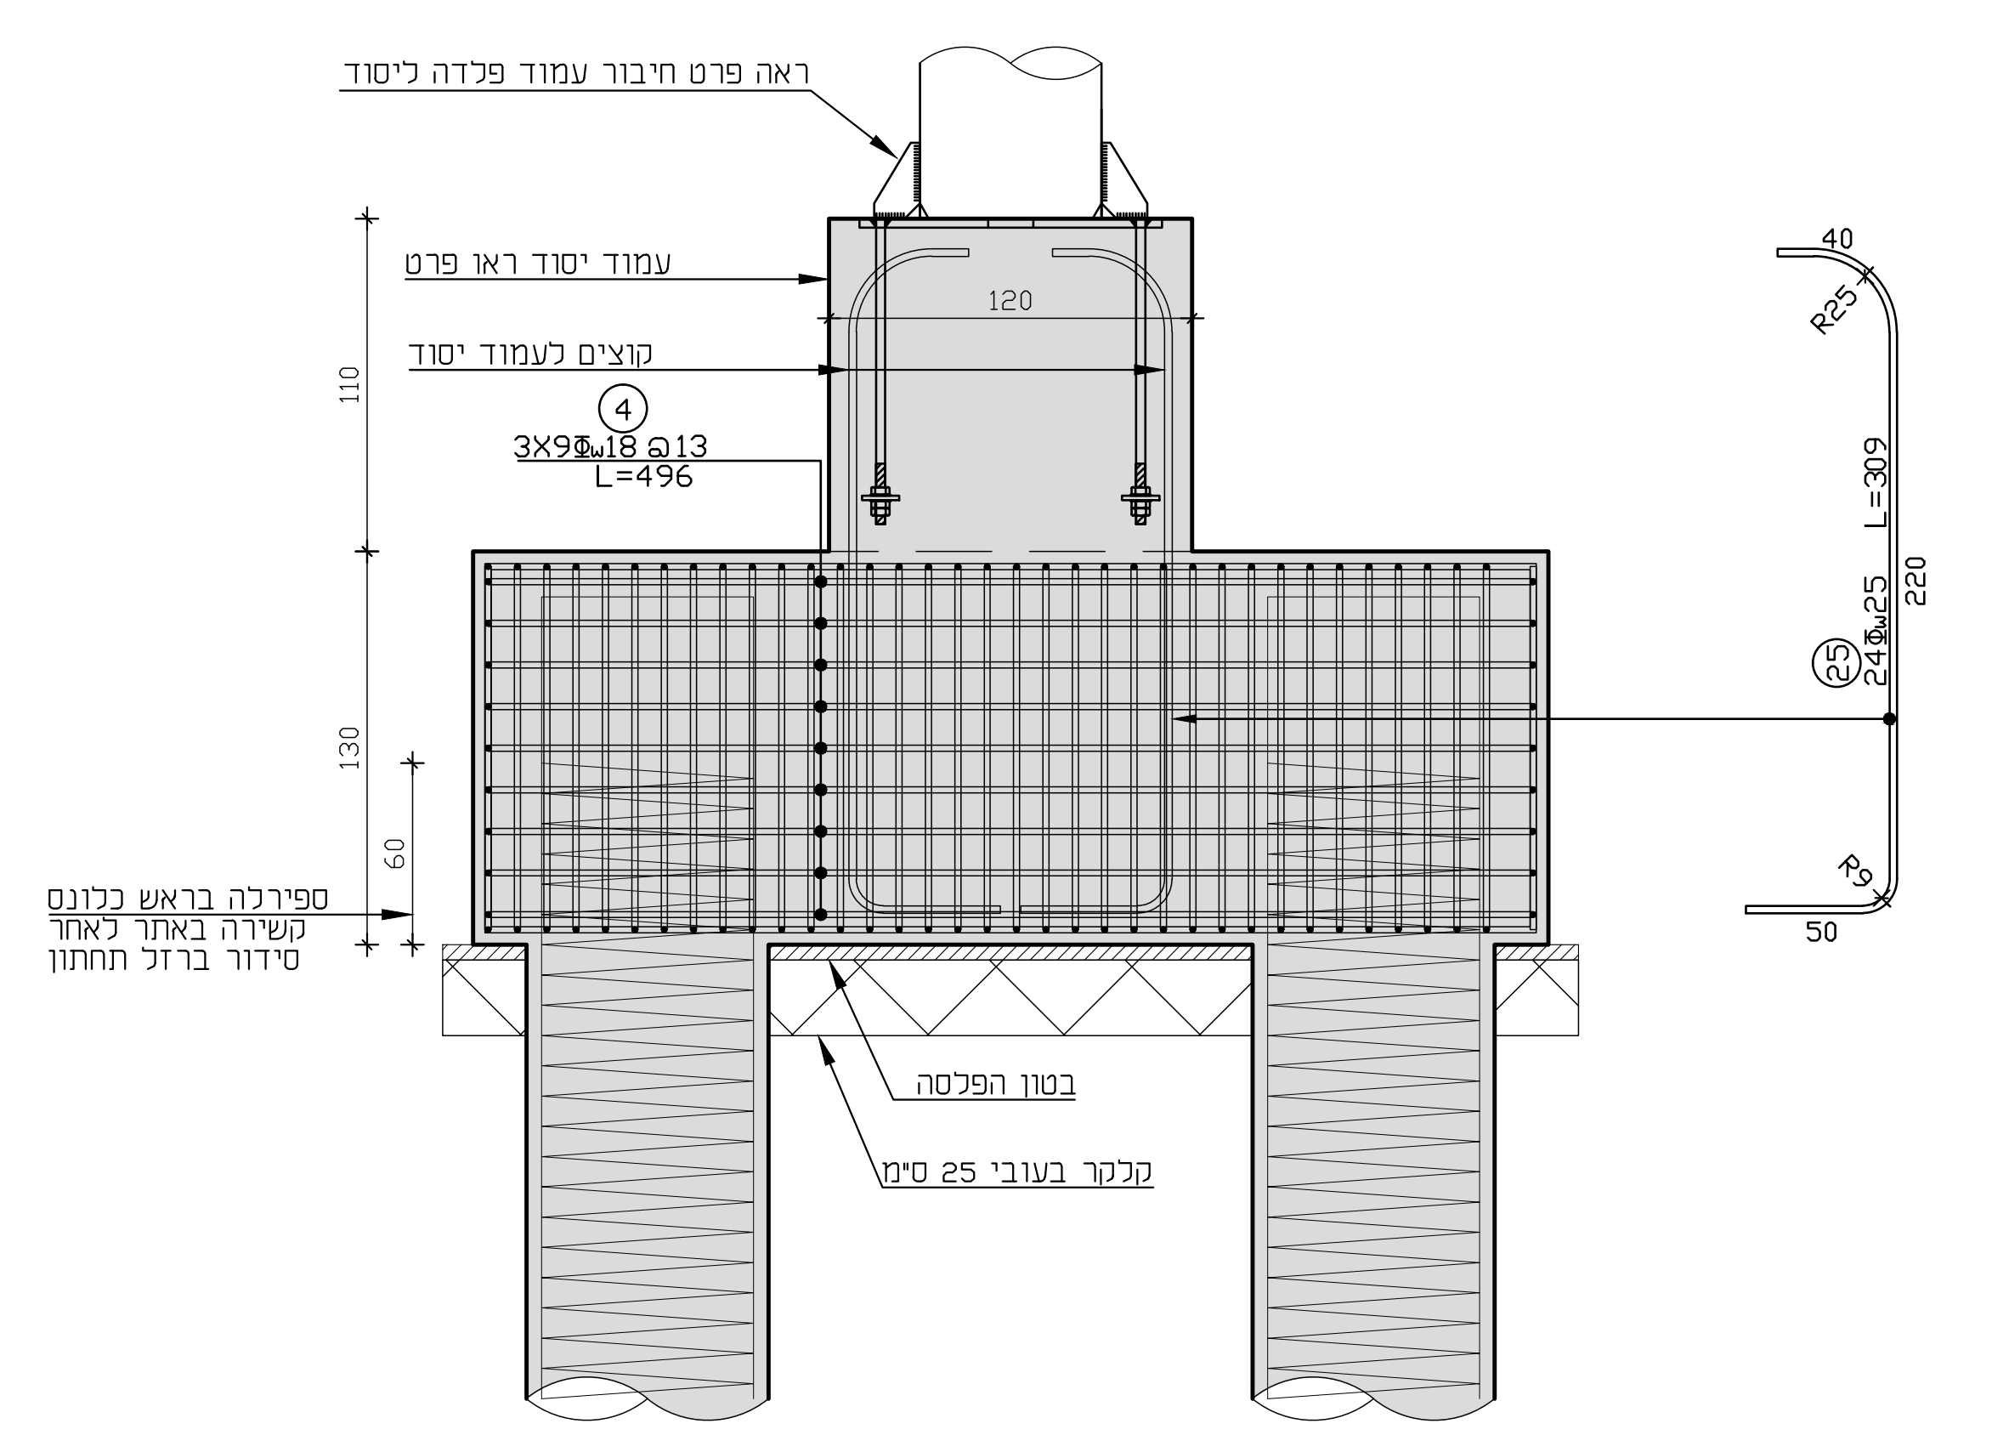

פרט עמוד יסוד בקוטר Ø120
קנ"מ 1:25

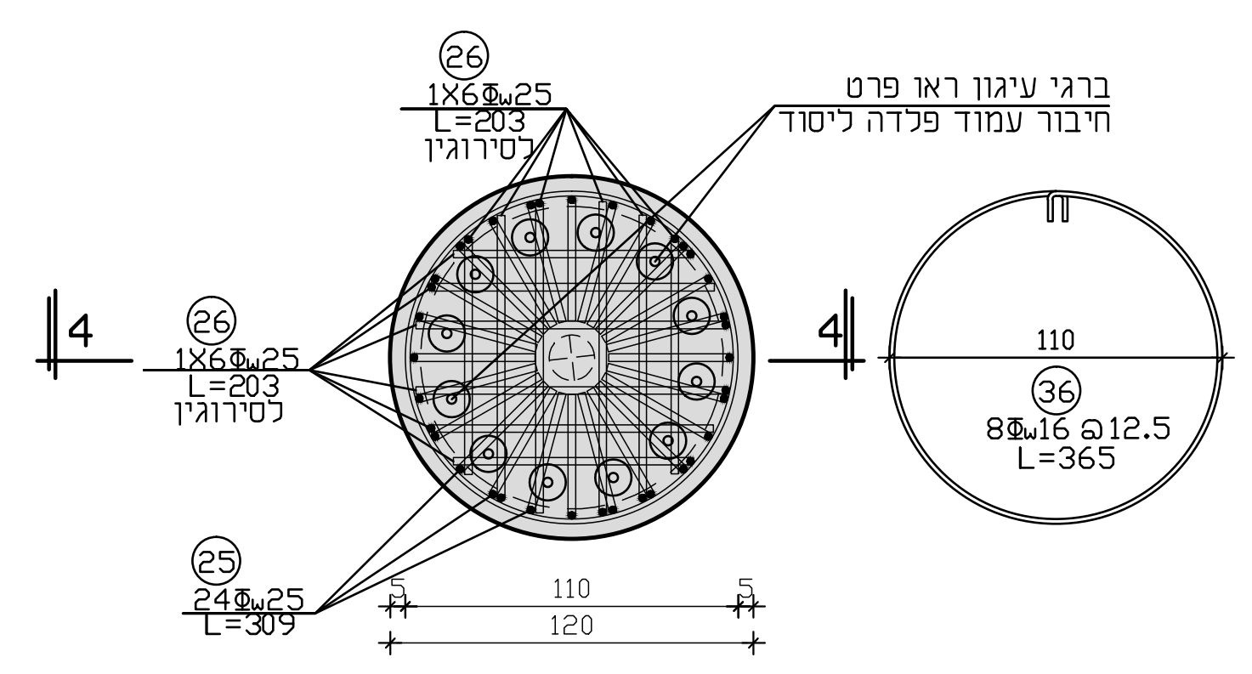

חתך 4-4
קנ"מ 1:25

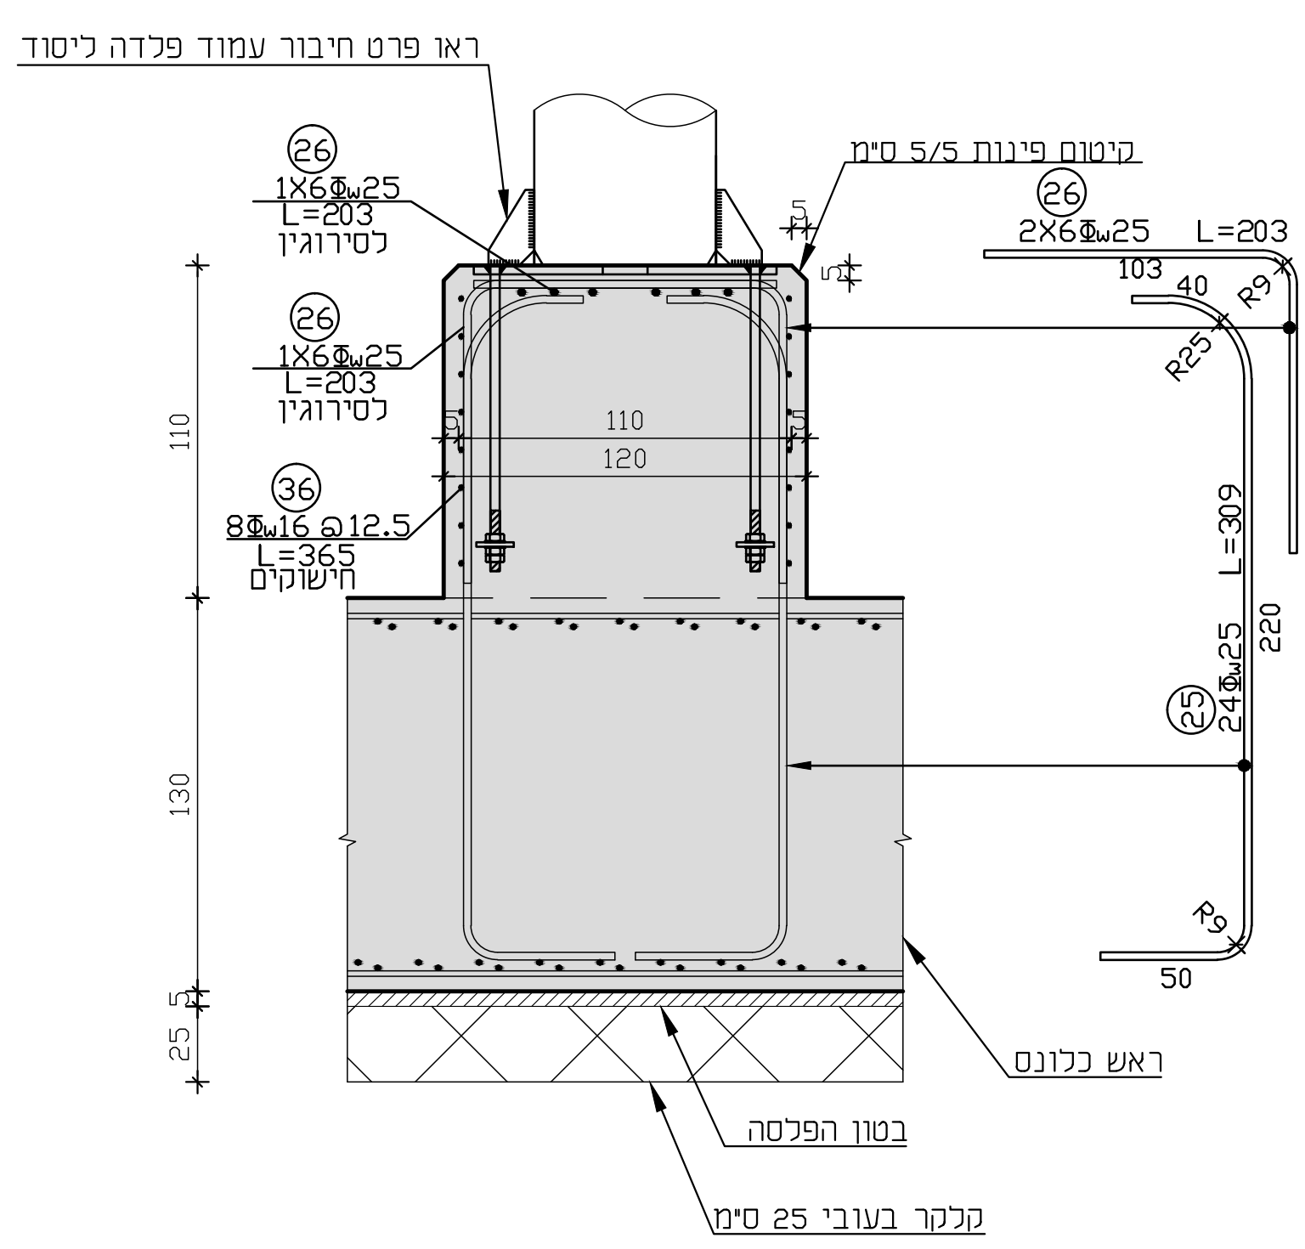

שלבי עבודה:

1. סידור הברזל התחתון של ראש הכלונס.
2. סידור הקוצים של עמוד היסוד (ברזל מסי 25).
3. הצבת פלטת הביסוס (יחד עם הברגים).
4. סידור הברזל העליון של ראש הכלונס.
5. יציקת ראש הכלונס.
   יש להימנע מהתזת בטון על הקוצים והברגים.
6. סידור החישוקים של עמוד היסוד (ברזל מסי 36).
7. סידור הברזל העליון של עמוד היסוד (ברזל מסי 26).
8. יציקת עמוד היסוד בתבנית עגולה חלקה לקבלת בטון חלק ונקי לפי החלטת האדריכל.

* יש להקפיד על דיוק המפלסים ומיקום פלטת הביסוס.
* יש להקפיד על פילוס תקין של פלטת הביסוס.

חתך בקורה 70/80
קנ"מ 1:20

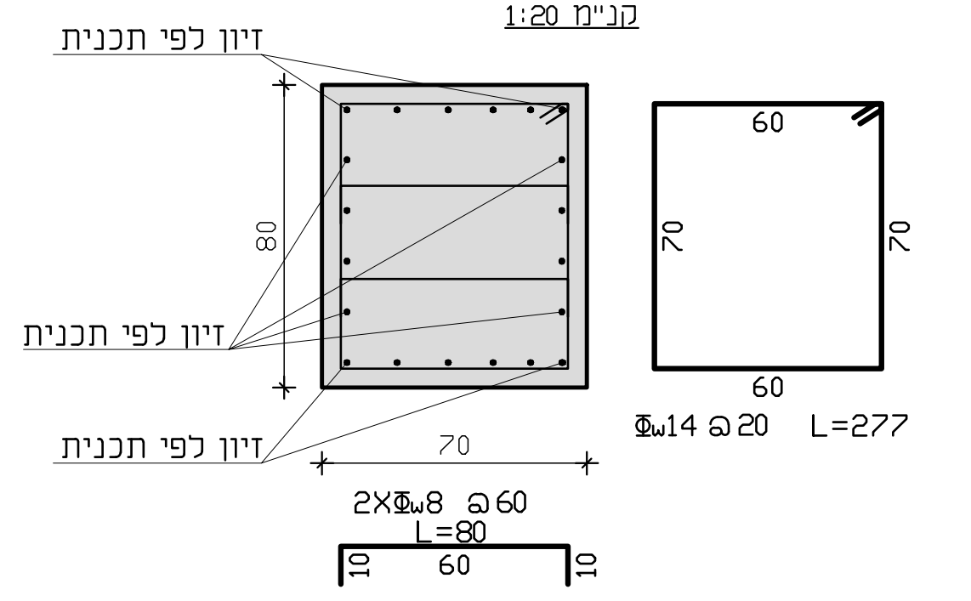

חתך בקורה 90/80
קנ"מ 1:20

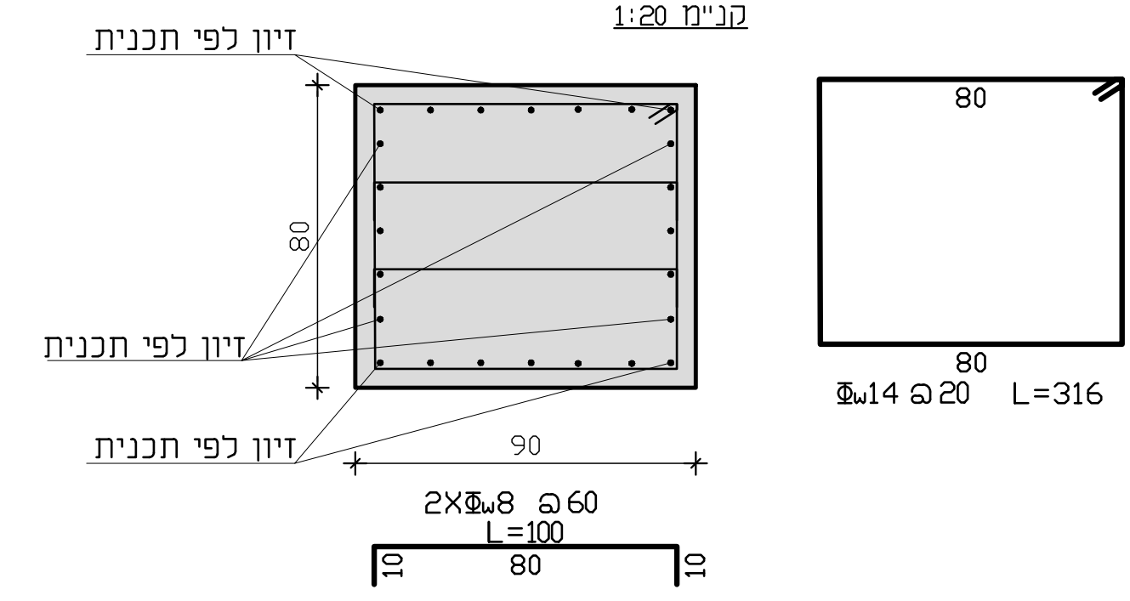

בטבלה שלהלן מפורטים עבור כל רכיבי הבטון בפרוייקט:
סוג הבטון והצמנט, סוג המבנה או הרכיב לפי טבלה 3.2 בת"י 466 חלק 1,
יחס מים-צמנט מקסימלית, כמות הצמנט המינימלית, דירוג הסומך ועובי בטון הכיסוי.

מס"ד	רכיב	סוג בטון/ סוג צמנט	סוג המבנה או הרכיב (טבלה 3.2 בת"י 466/1)	יחס מים-צמנט מקסי	כמות צמנט מינימלית (ק"ג מ"ק)	דירוג הסומך	עובי בטון הכיסוי (מ"מ)
1	בטון הפלסה	ב-30/ CEM-II 42.5N	-	-	-	S5	-
2	כלונסאות	ב-40/ CEM-I 52.5N	11	0.45	400	S8	75
3	ראשי כלונס קורות יסוד	ב-40/ CEM-II 42.5N	11	0.45	350	S5	50
4	קירות נציב	ב-40/ CEM-I 52.5N	11	0.45	350	S5	50
5	תקרות בטון הגבהות למעקות	ב-40/ CEM-II 42.5N	11	0.45	330	S5	30
6	טבלות גישה	ב-40/ CEM-I 52.5N	11	0.45	350	S5	50

מקרא

עמוד ממשיך	▭
עמוד מפסיק	▨
עמוד מתחיל	☐
חתך מקומי	⬚

הערות

1. סוג הבטון ב-40 מיני', אלא אם צוין אחרת.
2. זיון: ברזל עגול (Φ); ברזל מצולע רתיך פ-400D (Φw);
ברזל מצולע רתיך פ-500D (Φw);
רשתות מרותכות משוכות בקר (✱) לפי ת"י;
רשתות מרותכות מצולעות משוכות בקר (✱) לפי ת"י.
אין להשתמש בברזל פ-400D (Φw) אלא רק ב פ-500D (Φw)
אין להשתמש בברזל שאינו רתיך
אסור השימוש בברזל משוך בקר במרחב מוגן
3. אביזרי חשמל' אינס', מיזוג אויר וכו' ראה תכנית יועצים.
4. **כל הפלדה בדרגת פ-S355.**

המבצע אחראי לבדיקת המידות ולהתאמתן במקום. על המבצע לבקר את כל המידות ועל כל אי התאמה יש להודיע למתכנן לפני הביצוע. אין לקבוע מידות ע"י מדידה בתכנית. אין לבצע ללא היתר בנייה מתאים ותקף ו/או על פי תכנית שאיננה מסומנת כתכנית לביצוע.

יועצים

		S	
		R	
		Q	
		P	
		O	
		N	
אינסטי'		M	
אתר		L	
מזמין		K	
מתאם		J	
קרקע		I	
מיזוג אויר		H	
מעליות		G	
בטיחות		F	
חשמל		E	
קונסטי'		D	
תנועה		C	
פתוח		B	
אדריכל		A	
תאריך			00.00.00

שינויים

מסי	תאריך	שינוי
6	00.00.00	___
5	00.00.00	___
4	00.00.00	___
3	00.00.00	___
2	00.00.00	___
1	00.00.00	___
0	00.00.00	___

מתחם ה-1000 ג'
גשר הו"ר בפארק

היזם
חכ"ל ראשון לציון

אדריכלות
צורנמל-טרנר

תאור

שם התכנית:
תכנית יסודות
ראשי כלונסאות וקורות יסוד

שם הקובץ:
??833.1-01-20-FOUNDATION

מספר התכנית: 833.1-01A-20
תאריך עדכון: 25.05.2022

תכנן: שי לוי
שרטט: שי לוי
אישר: דוין/ברק
שינוי מס: 00

לעיון/לאישור ☐
למכרז ☐
לביצוע ☒
קנה המידה: 1:25

רוקח & אשכנזי
מהנדסים יועצים בע"מ
רח' בורלא 52 ת"א E-mail: RA@RA-ENG.COM
טל': 03-6994427 פקס: 03-6995808
WWW.RA-ENG.COM