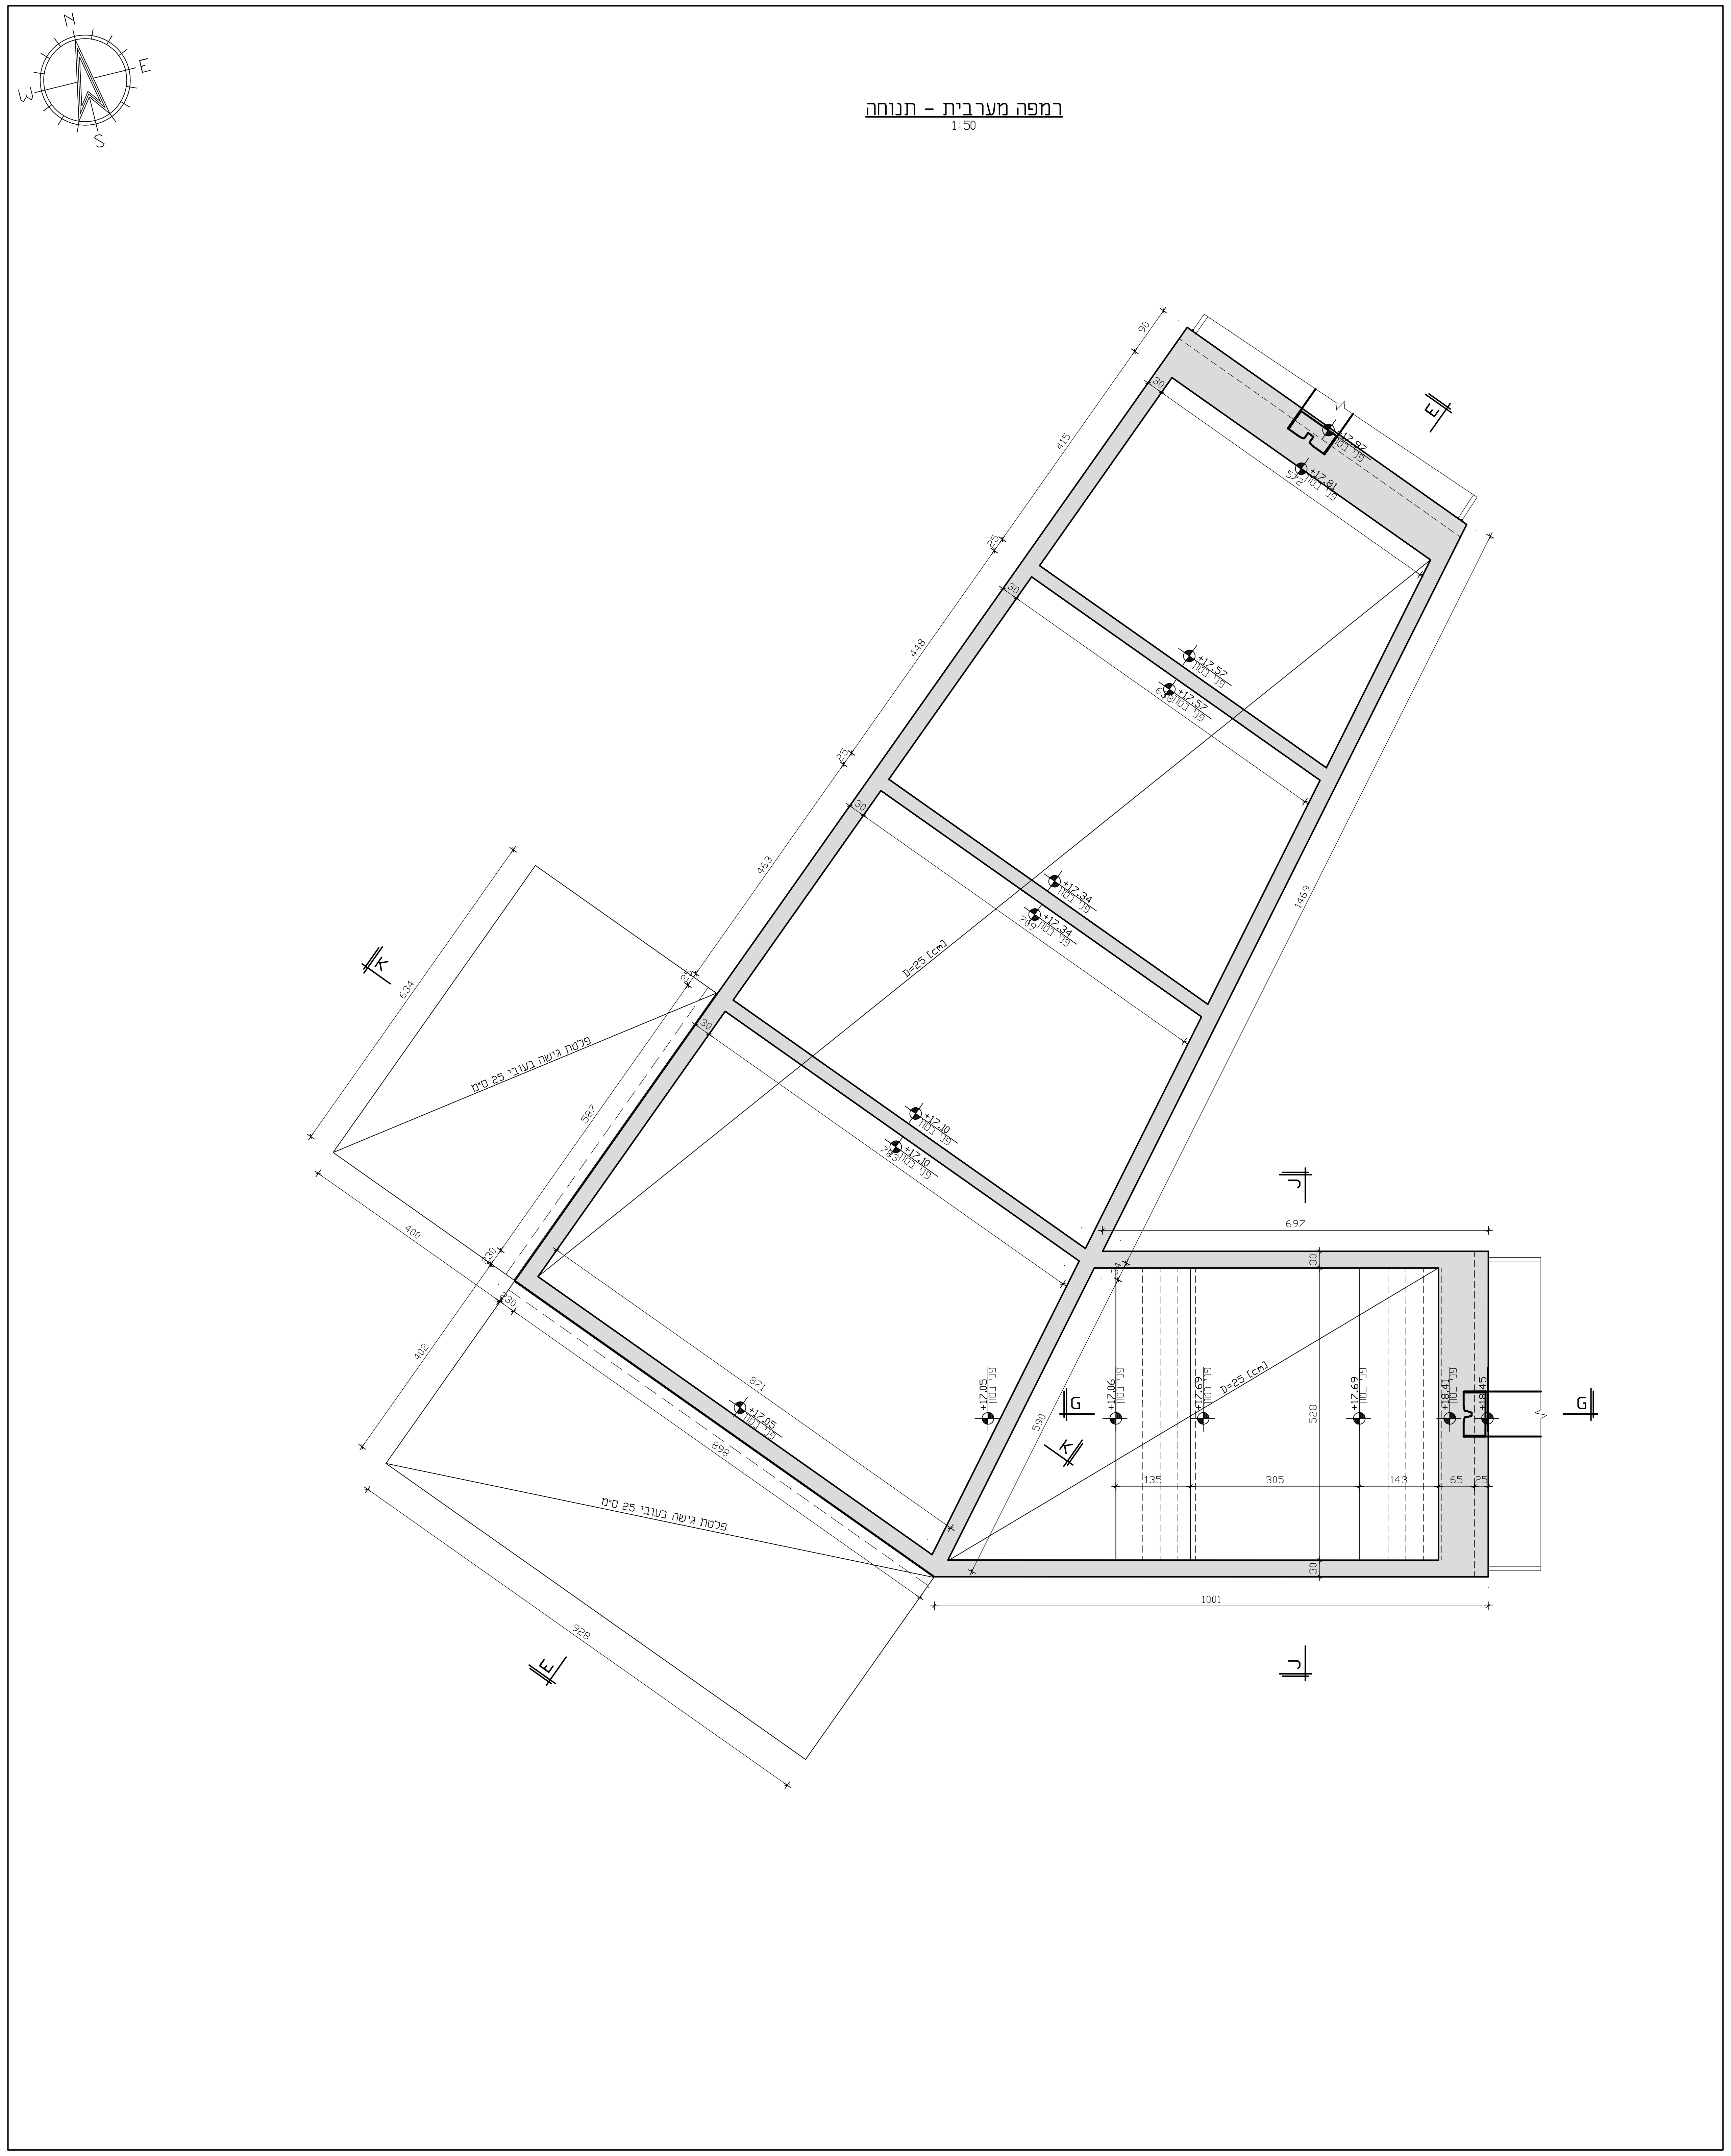

רמפה מערבית - תנוחה

1:50

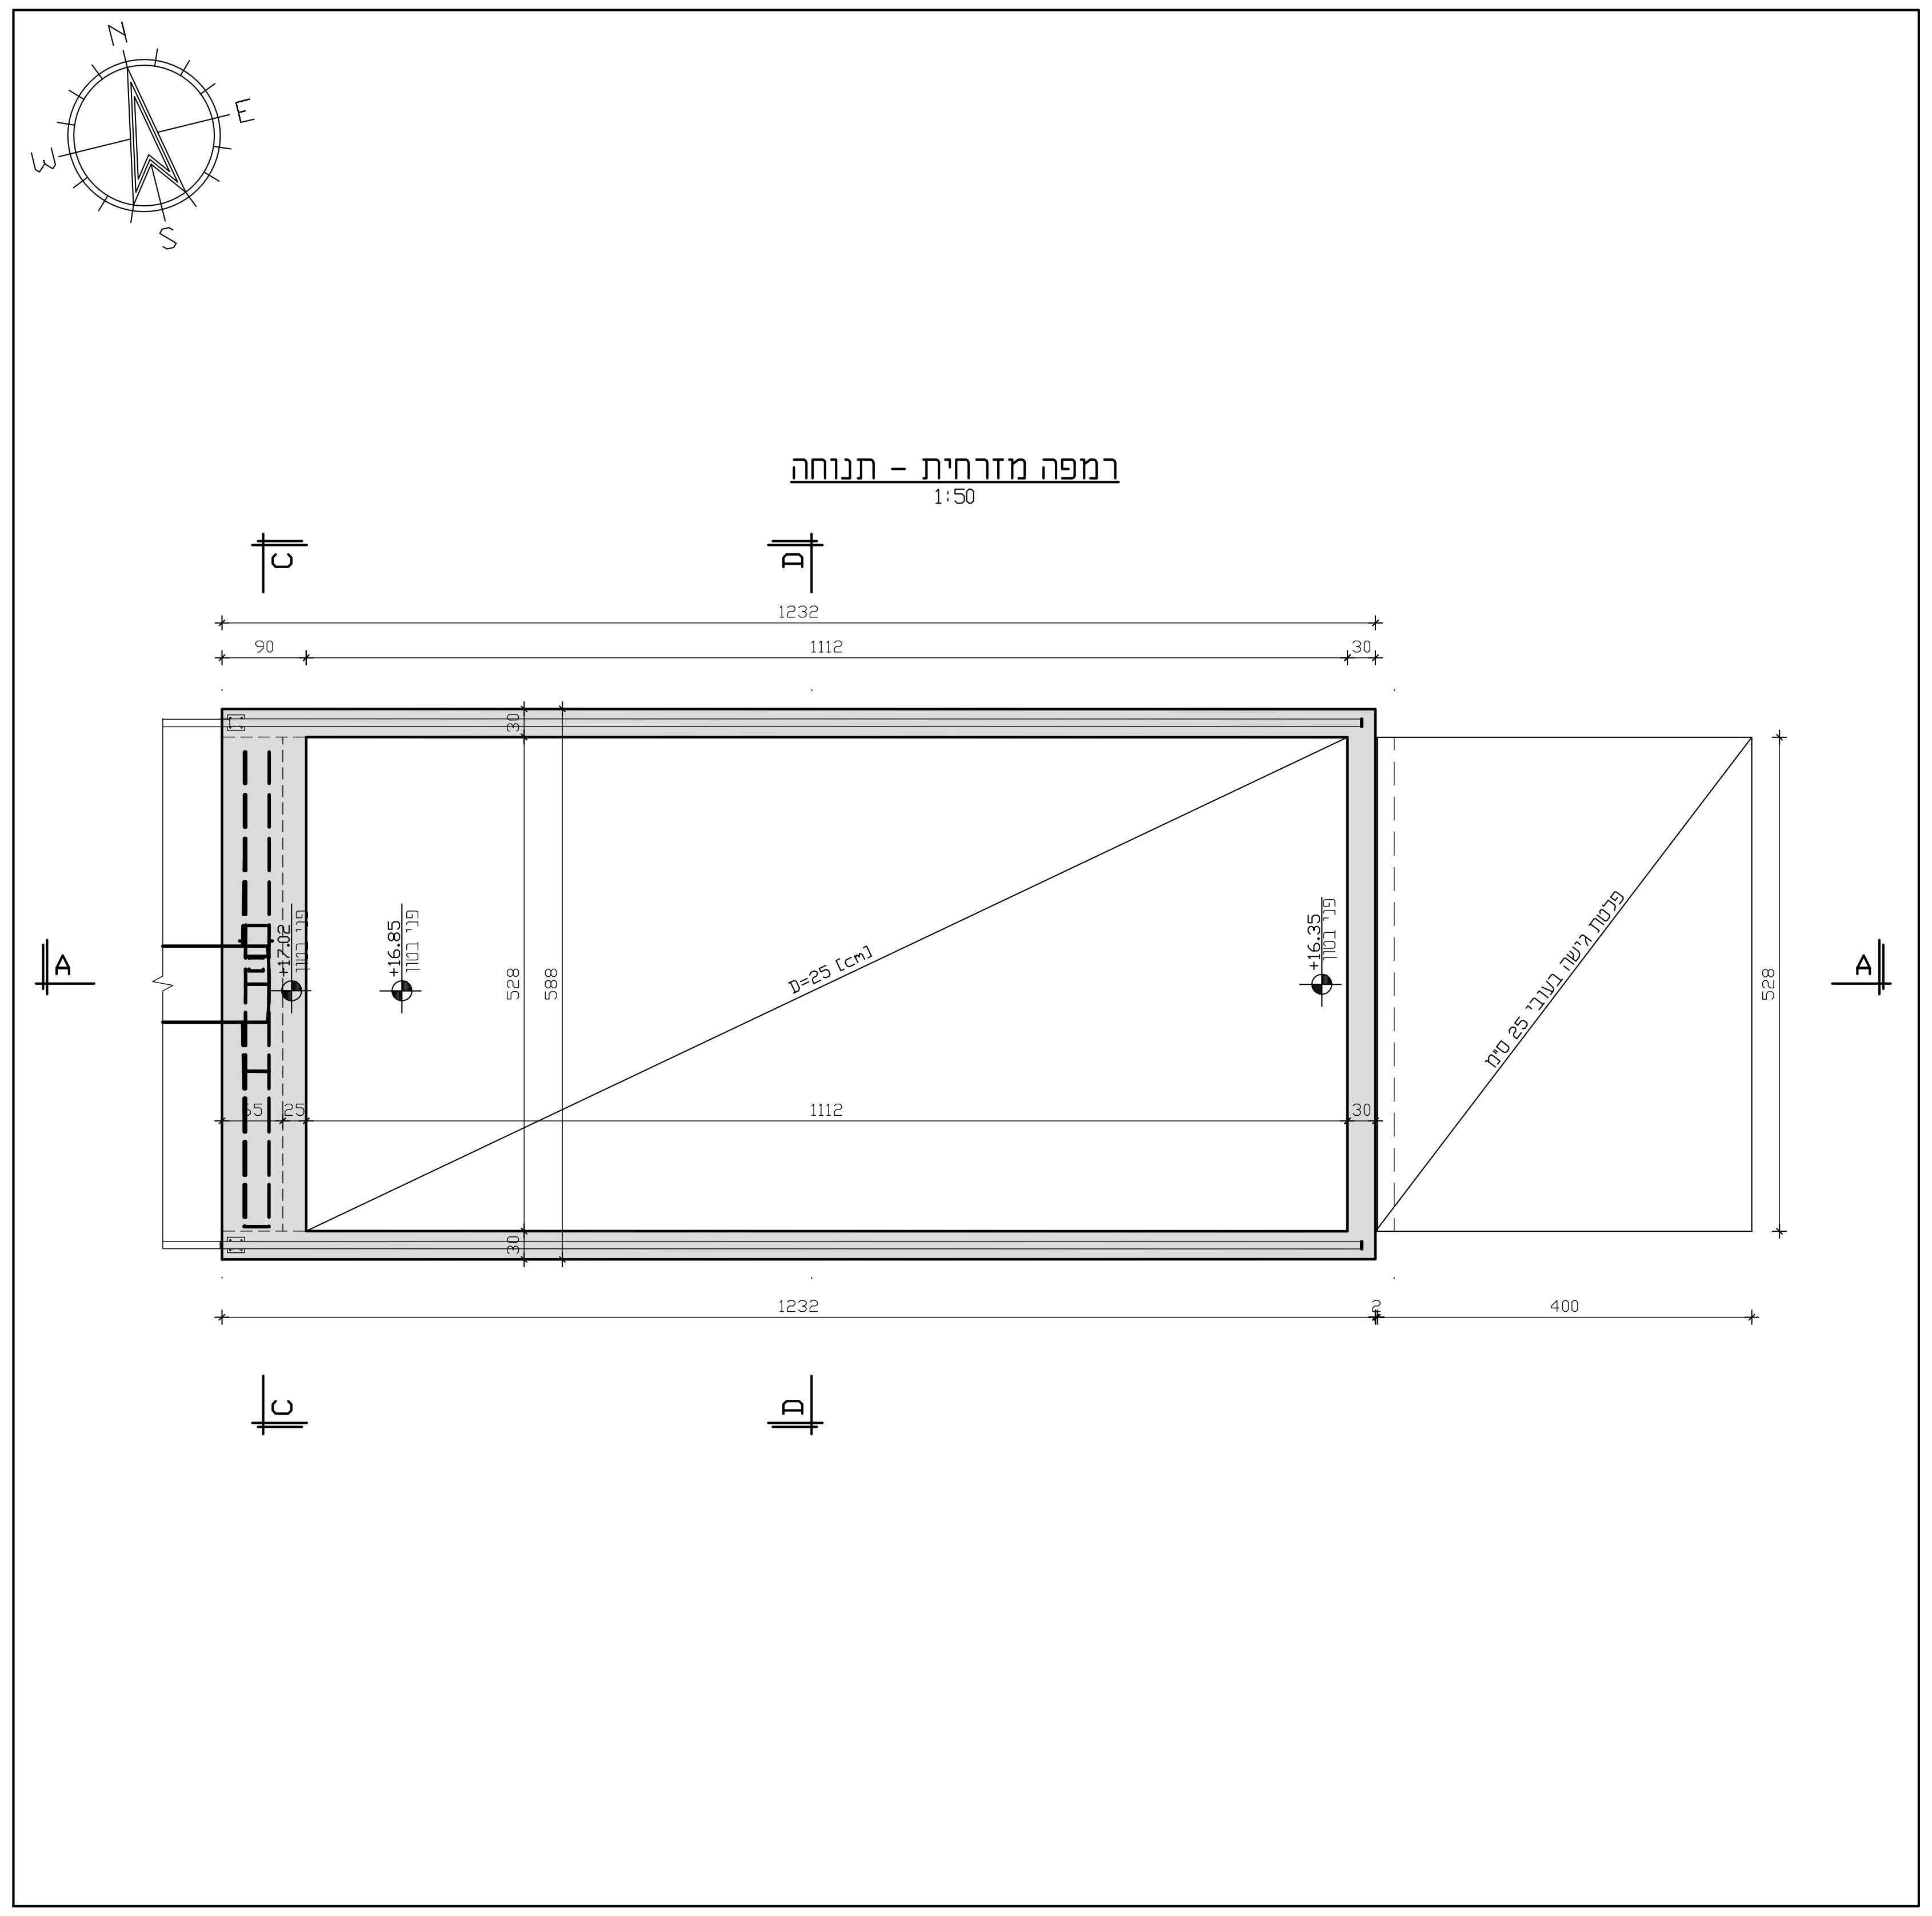

רמפה מזרחית - תנוחה

1:50

עמוד ממשיך	▨
עמוד מפסיק	▧
עמוד מתחיל	☐
חתך מקומי	▒

סימנים

הערות

1. סוג הבטון ב-40 מינ׳, אלא אם צוין אחרת.
2. **יעשה שימוש בברזל מצולע רתיך בלבד מסוג פ-500ר (Φw).**
   אין להשתמש בברזל פ-400ר (Φw).
   רשתות מרותכות יהיו משוכות בקר (*) לפי ת״י;
   רשתות מרותכות מצולעות יהיו משוכות בקר (*) לפי ת״י.
   אין להשתמש בברזל שאינו רתיך.
   אסור השימוש בברזל משוך בקר במרחב מוגן.
3. אביזרי חשמלי אינסט׳, מיזוג אויר וכו׳ ראה תכנית יועצים.
4. **כל הפלדה בדרגת מ-S355.**

המבצע אחראי לבדיקת המידות ולהתאמתן במקום. על המבצע לבקר את כל המידות ועל כל אי התאמה יש להודיע למתכנן לפני הביצוע. אין לקבוע מידות ע״י מדידה בתכנית. אין לבצע ללא היתר בנייה מתאים ותקף ו/או על פי תכנית שאיננה מסומנת כתכנית לביצוע.

הפצה

		S									
		R									
		Q									
		P									
		O									
		N									
אינסטי		M									
אתר		L									
מזמין		K									
מתאם		J									
קרקע		I									
מיזוג אויר		H									
מעליות		G									
בטיחות		F									
חשמל		E									
קונסטי		D									
תנועה		C									
פתוח		B									
אדריכל		A									
תאריך			00.00.00								

שינויים

מסי	תאריך	שינוי
6	00.00.00	___
5	00.00.00	___
4	00.00.00	___
3	00.00.00	___
2	00.00.00	___
1	00.00.00	___
0	00.00.00	___

מתחם ה-1000 ג׳
גשר הו״ר בפארק

היזם

חכ״ל ראשון לציון

אדריכלות

צורנמל-טרנר

תאור

שם התכנית:

תוכנית רמפות בטון
תבניות

שם הקובץ:

833.1-02-20-RAMPS

מספר התכנית:

833.1-02-20

תאריך עדכון:

25.05.2022

תכנן:	שרטט:	אישר:	שינוי מס׳:
שי לוי	שי לוי	דוין/ברק	00
לעיון/לאישור	למכרז	לביצוע	קנה המידה:
☐	☐	☒	1:50

רוקח & אשכנזי
מהנדסים יועצים בע״מ
רח׳ בורלא 52 ת״א E-mail: RA@RA-ENG.COM
טל׳: 03-6994427 פקס: 03-6995808
WWW.RA-ENG.COM

בטבלה שלהלן מפורטים עבור כל רכיבי הבטון בפרוייקט:
סוג הבטון והצמנט, סוג המבנה או הרכיב לפי טבלה 3.2 בת״י 466 חלק 1,
יחס מים-צמנט מקסימלית, כמות הצמנט המינימלית, דירוג הסומך ועובי בטון הכיסוי.

מס״ד	רכיב	סוג בטון/ סוג צמנט	סוג המבנה או הרכיב (טבלה 3.2 בת״י 466/1)	יחס מים-צמנט מקסי	כמות צמנט מינימלית (ק״ג מ״ק)	דירוג הסומך	עובי בטון הכיסוי (מ״מ)
1	בטון הפלסה	ב-30/ CEM-II 42.5N	-	-	-	S5	-
2	כלונסאות	ב-40/ CEM-I 52.5N	11	0.45	400	S8	75
3	ראשי כלונס קורות יסוד	ב-40/ CEM-II 42.5N	11	0.45	350	S5	50
4	קירות נציב	ב-40/ CEM-I 52.5N	11	0.45	350	S5	50
5	תקרות בטון הגבהות למעקות	ב-40/ CEM-II 42.5N	11	0.45	330	S5	30
6	טבלות גישה	ב-40/ CEM-I 52.5N	11	0.45	350	S5	50

25.05.2022 60\NCons\NEW\833.1-00-20-GM רגל הולכי גשר - ג מתחם האלף מתחם P:\PROJECTS\833.1