חתך G-G
1:50

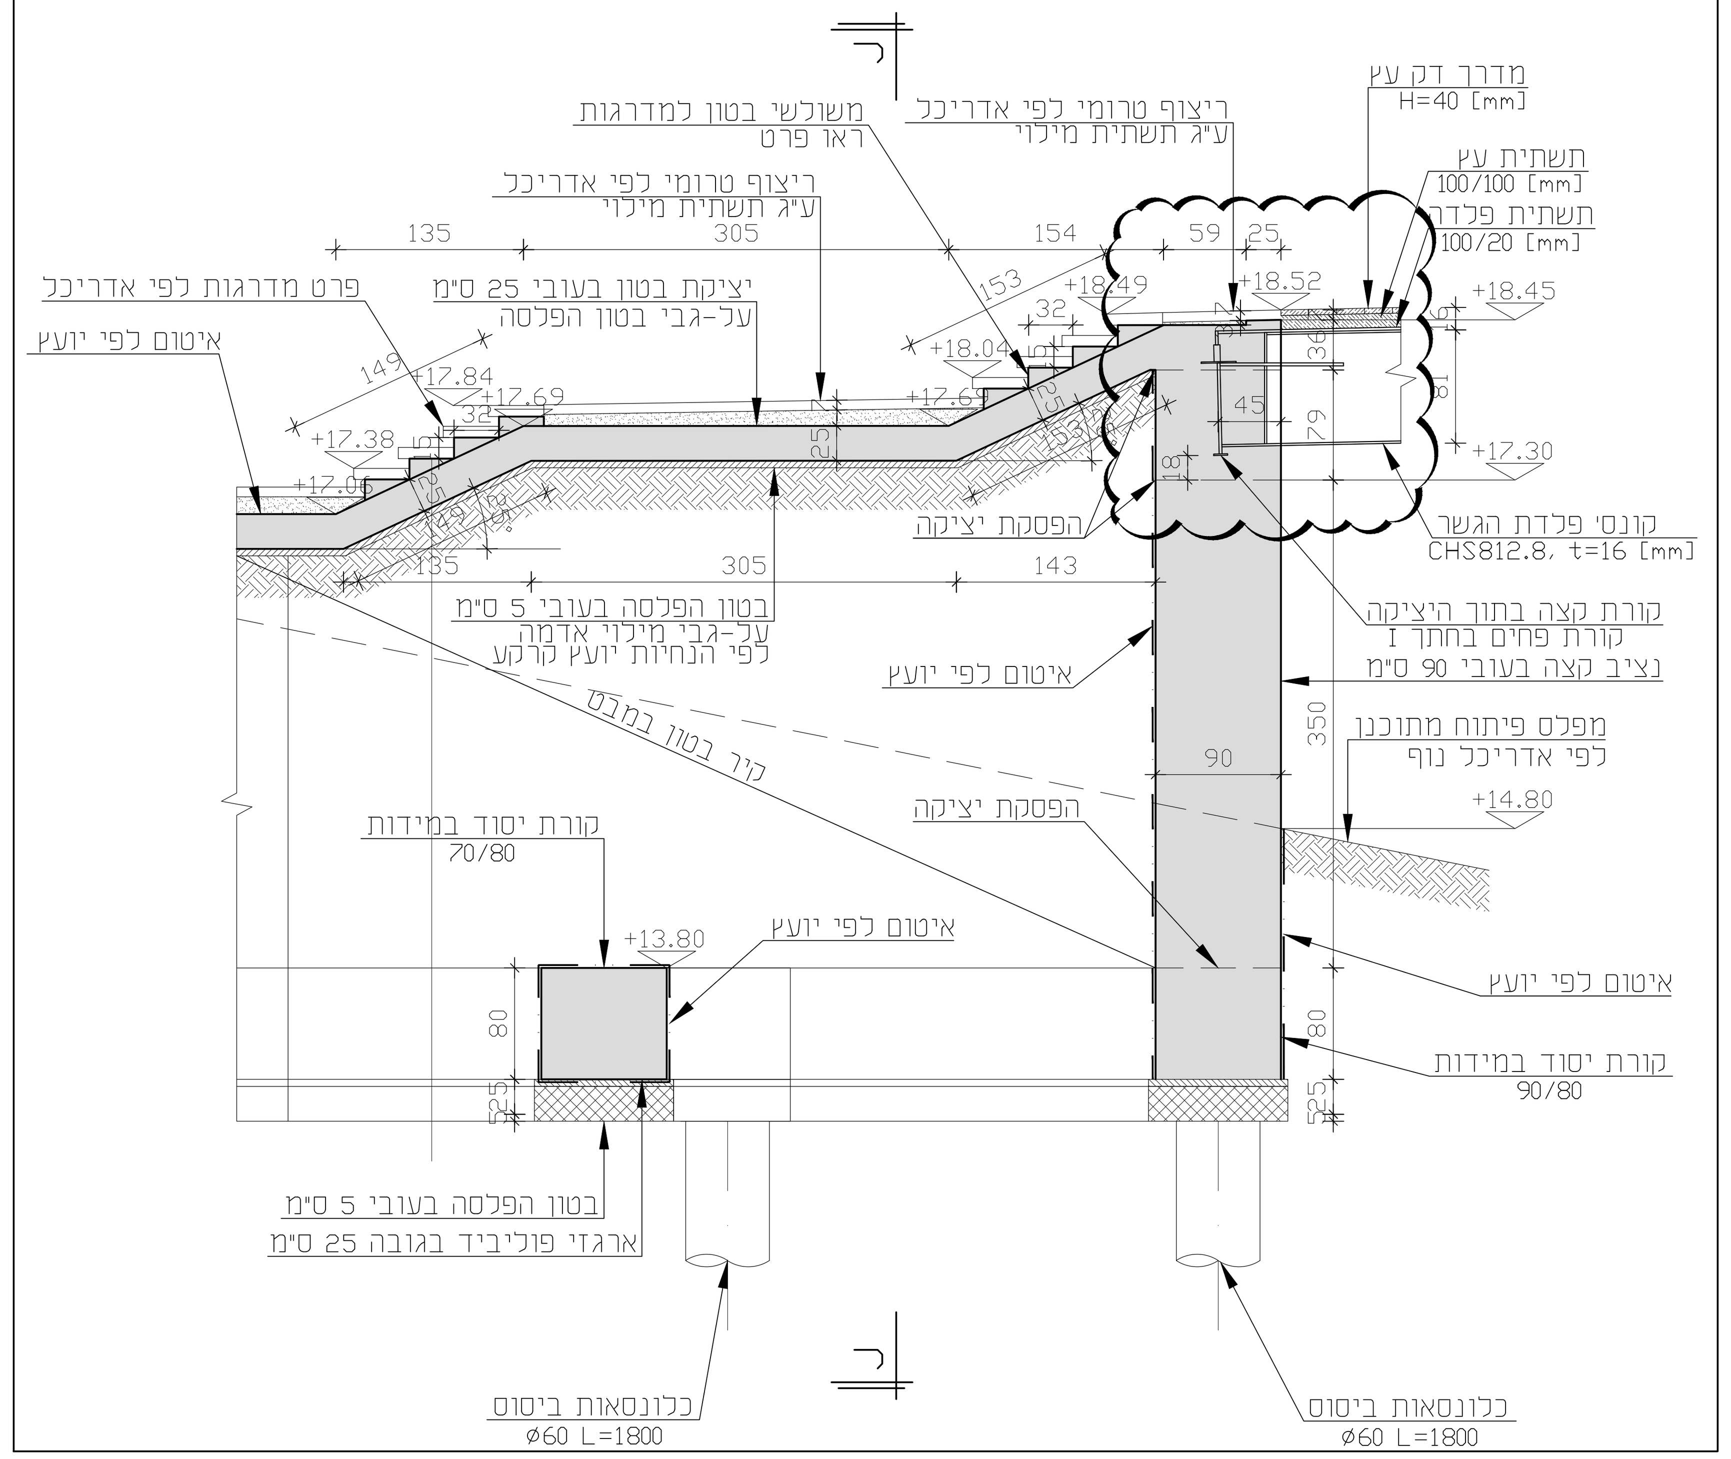

חתך K-K
1:50

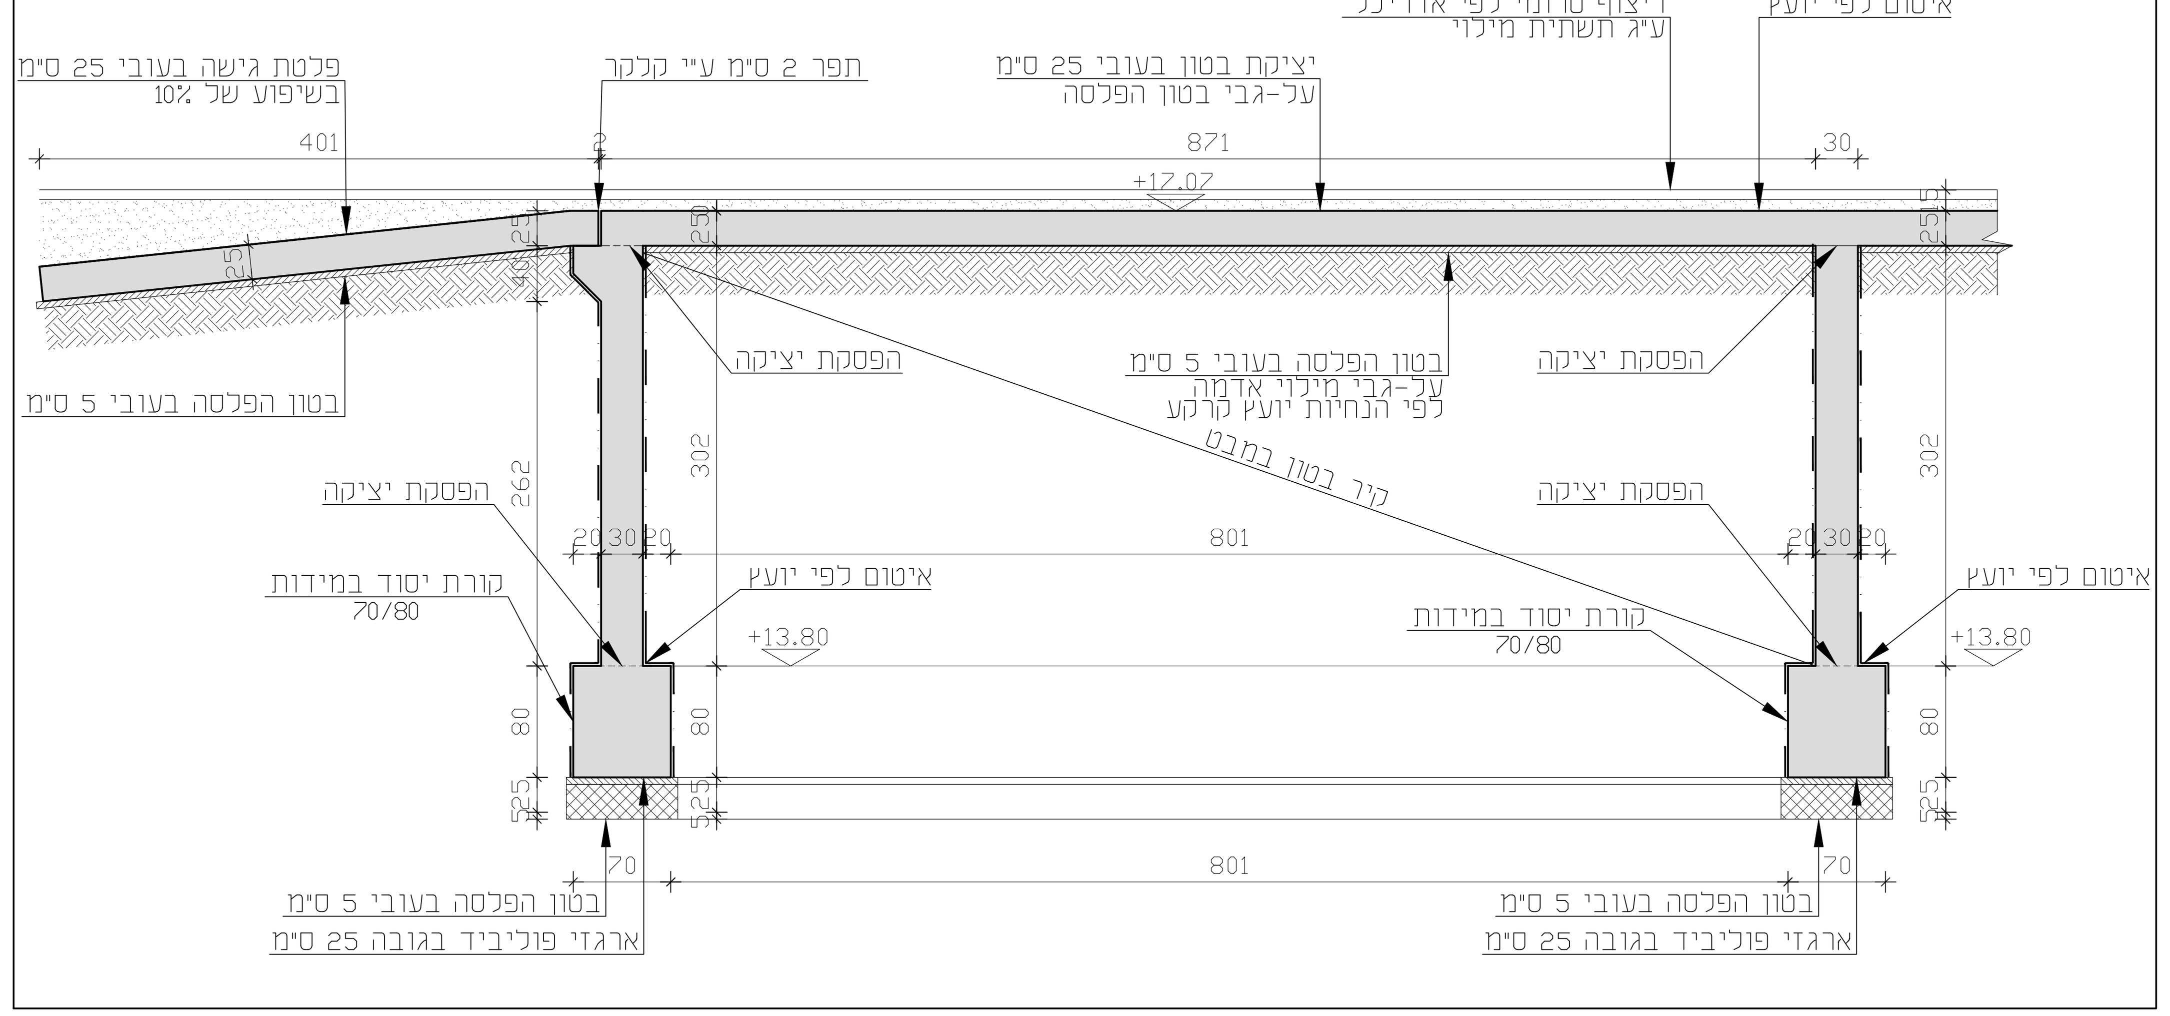

חתך J-J
1:50

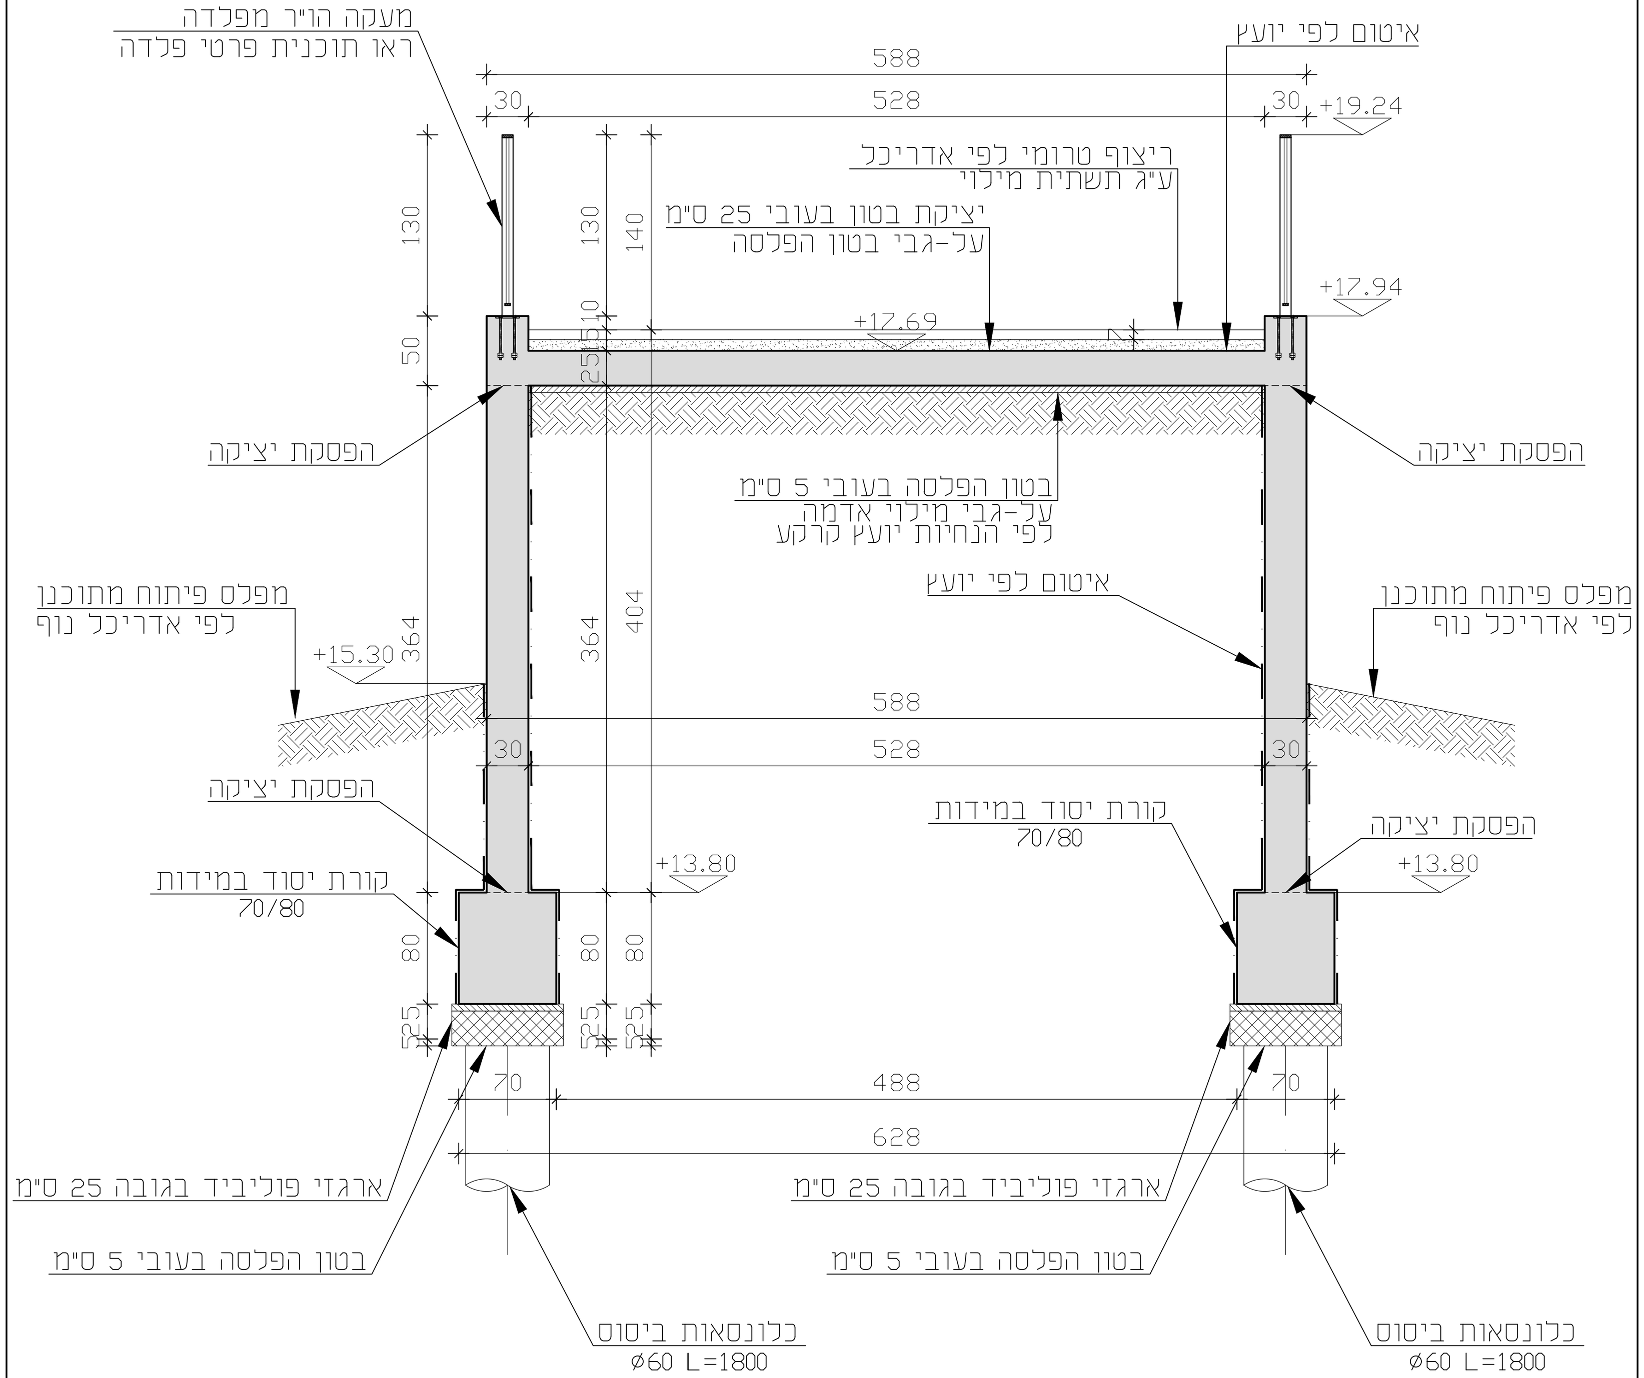

חתך E-E
1:50

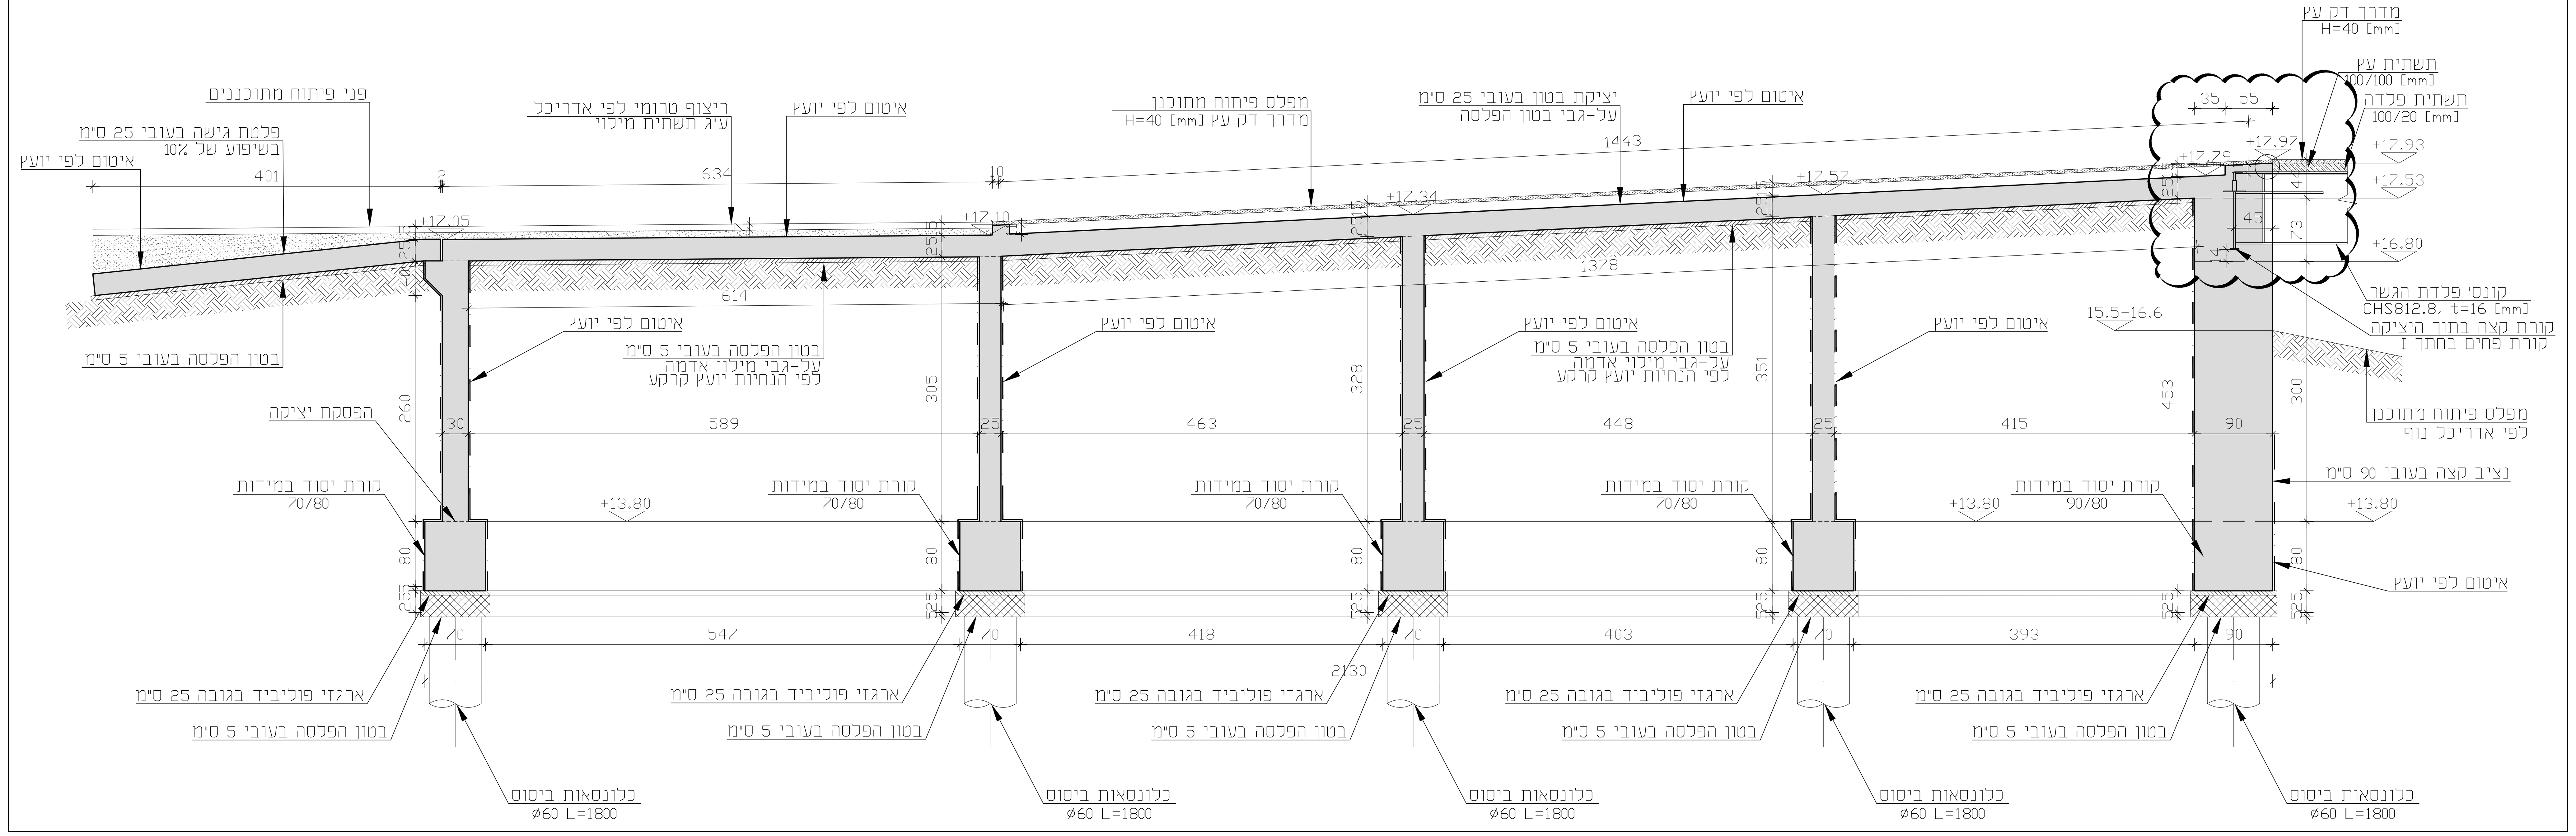

שלבי ביצוע

1. יציקת קורות הראש וסידור הקוצים לקירות.
2. השלמת הסידור הזיון בקירות.
3. יציקת הקירות עד לגובה הפסקות היציקה, כמתואר בתוכניות.
4. איטום הקירות וראשי וקורות הראש.
5. ביצוע עבודות הכנה עבור יציקת רצפת הבטון:
   5.1. מילוי קרקע משני צידי הקירות, באופן סימולטני, עד לגובה המתוכנן.
   5.2. ראשית יש להתחיל למלא את הקרקע מהצד החיצוני של הקירות.
   המילוי מהצד החיצוני יהיה עד למפלסי הפיתוח הסופיים המתוכננים.
   המילוי יבוצע עד למרחק של לפחות 3 מ' מהקירות.
   5.3. בו-זמנית (באופן סימולטני) יש למלא את הקרקע בתוך הרמפה (מתחת לרצפה).
   5.4. בסיום המילוי יש לבצע הידוק ופילוס לקרקע.
   5.5. יציקת בטון הפלסה על-גבי הקרקע.
6. סידור הזיון ברצפה ויציקת הרצפה.
7. איטום פני הרצפה.
8. יישום גמרים בהתאם לפרטי האדריכל.

*מילוי הקירות יבוצע באופן סימולטני בלבד.
ראו סעיפים מס' 5.3 - 5.1.

<u>בטבלה שלהלן מפורטים עבור כל רכיבי הבטון בפרוייקט:</u>
סוג הבטון והצמנט, סוג המבנה או הרכיב לפי טבלה 3.2 בת"י 466 חלק 1,
יחס מים-צמנט מקסימלית, כמות הצמנט המינימלית, דירוג הסומך ועובי בטון הכיסוי.

מס"ד	רכיב	סוג בטון/ סוג צמנט	סוג המבנה או הרכיב (טבלה 3.2 בת"י 466/1)	יחס מים-צמנט מקסי'	כמות צמנט מינימלית (ק"ג מ"ק)	דירוג הסומך	עובי בטון הכיסוי (מ"מ)
1	בטון הפלסה	ב-30/ CEM-II 42.5N	-	-	-	S5	-
2	כלונסאות	ב-40/ CEM-I 52.5N	11	0.45	400	S8	75
3	ראשי כלונס קורות יסוד	ב-40/ CEM-II 42.5N	11	0.45	350	S5	50
4	קירות נציב	ב-40/ CEM-I 52.5N	11	0.45	350	S5	50
5	תקרות בטון הגבהות למעקות	ב-40/ CEM-II 42.5N	11	0.45	330	S5	30
6	טבלות גישה	ב-40/ CEM-I 52.5N	11	0.45	350	S5	50

מתחם ה-1000 ג'
גשר הו"ר בפארק

היזם: חכ"ל ראשון לציון

אדריכלות: צורנמל-טרנר

שם התכנית: חתכים רמפה מערבית תבניות

שם הקובץ: 833.1-02-20-RAMPS

מספר התכנית: 833.1-03-20

תאריך עדכון: 10.11.2022

תכנן:	שרטט:	אישר:	שינוי מס':
שי לוי	שי לוי	דוין/ברק	01

לעיון/לאישור	למכרז	לביצוע	קנה המידה:
☐	☐	☒	1:50

רוקח & אשכנזי
מהנדסים יועצים בע"מ
רח' בורלא 52 ת"א E-mail: RA@RA-ENG.COM
טל': 03-6994427 פקס: 03-6995808
WWW.RA-ENG.COM

10.11.2022 60\תCons\NEW\833.1-00-20-GM גשר הולכי רגל - מתחם ג מתחם האלף P:\PROJECTS\833.1