
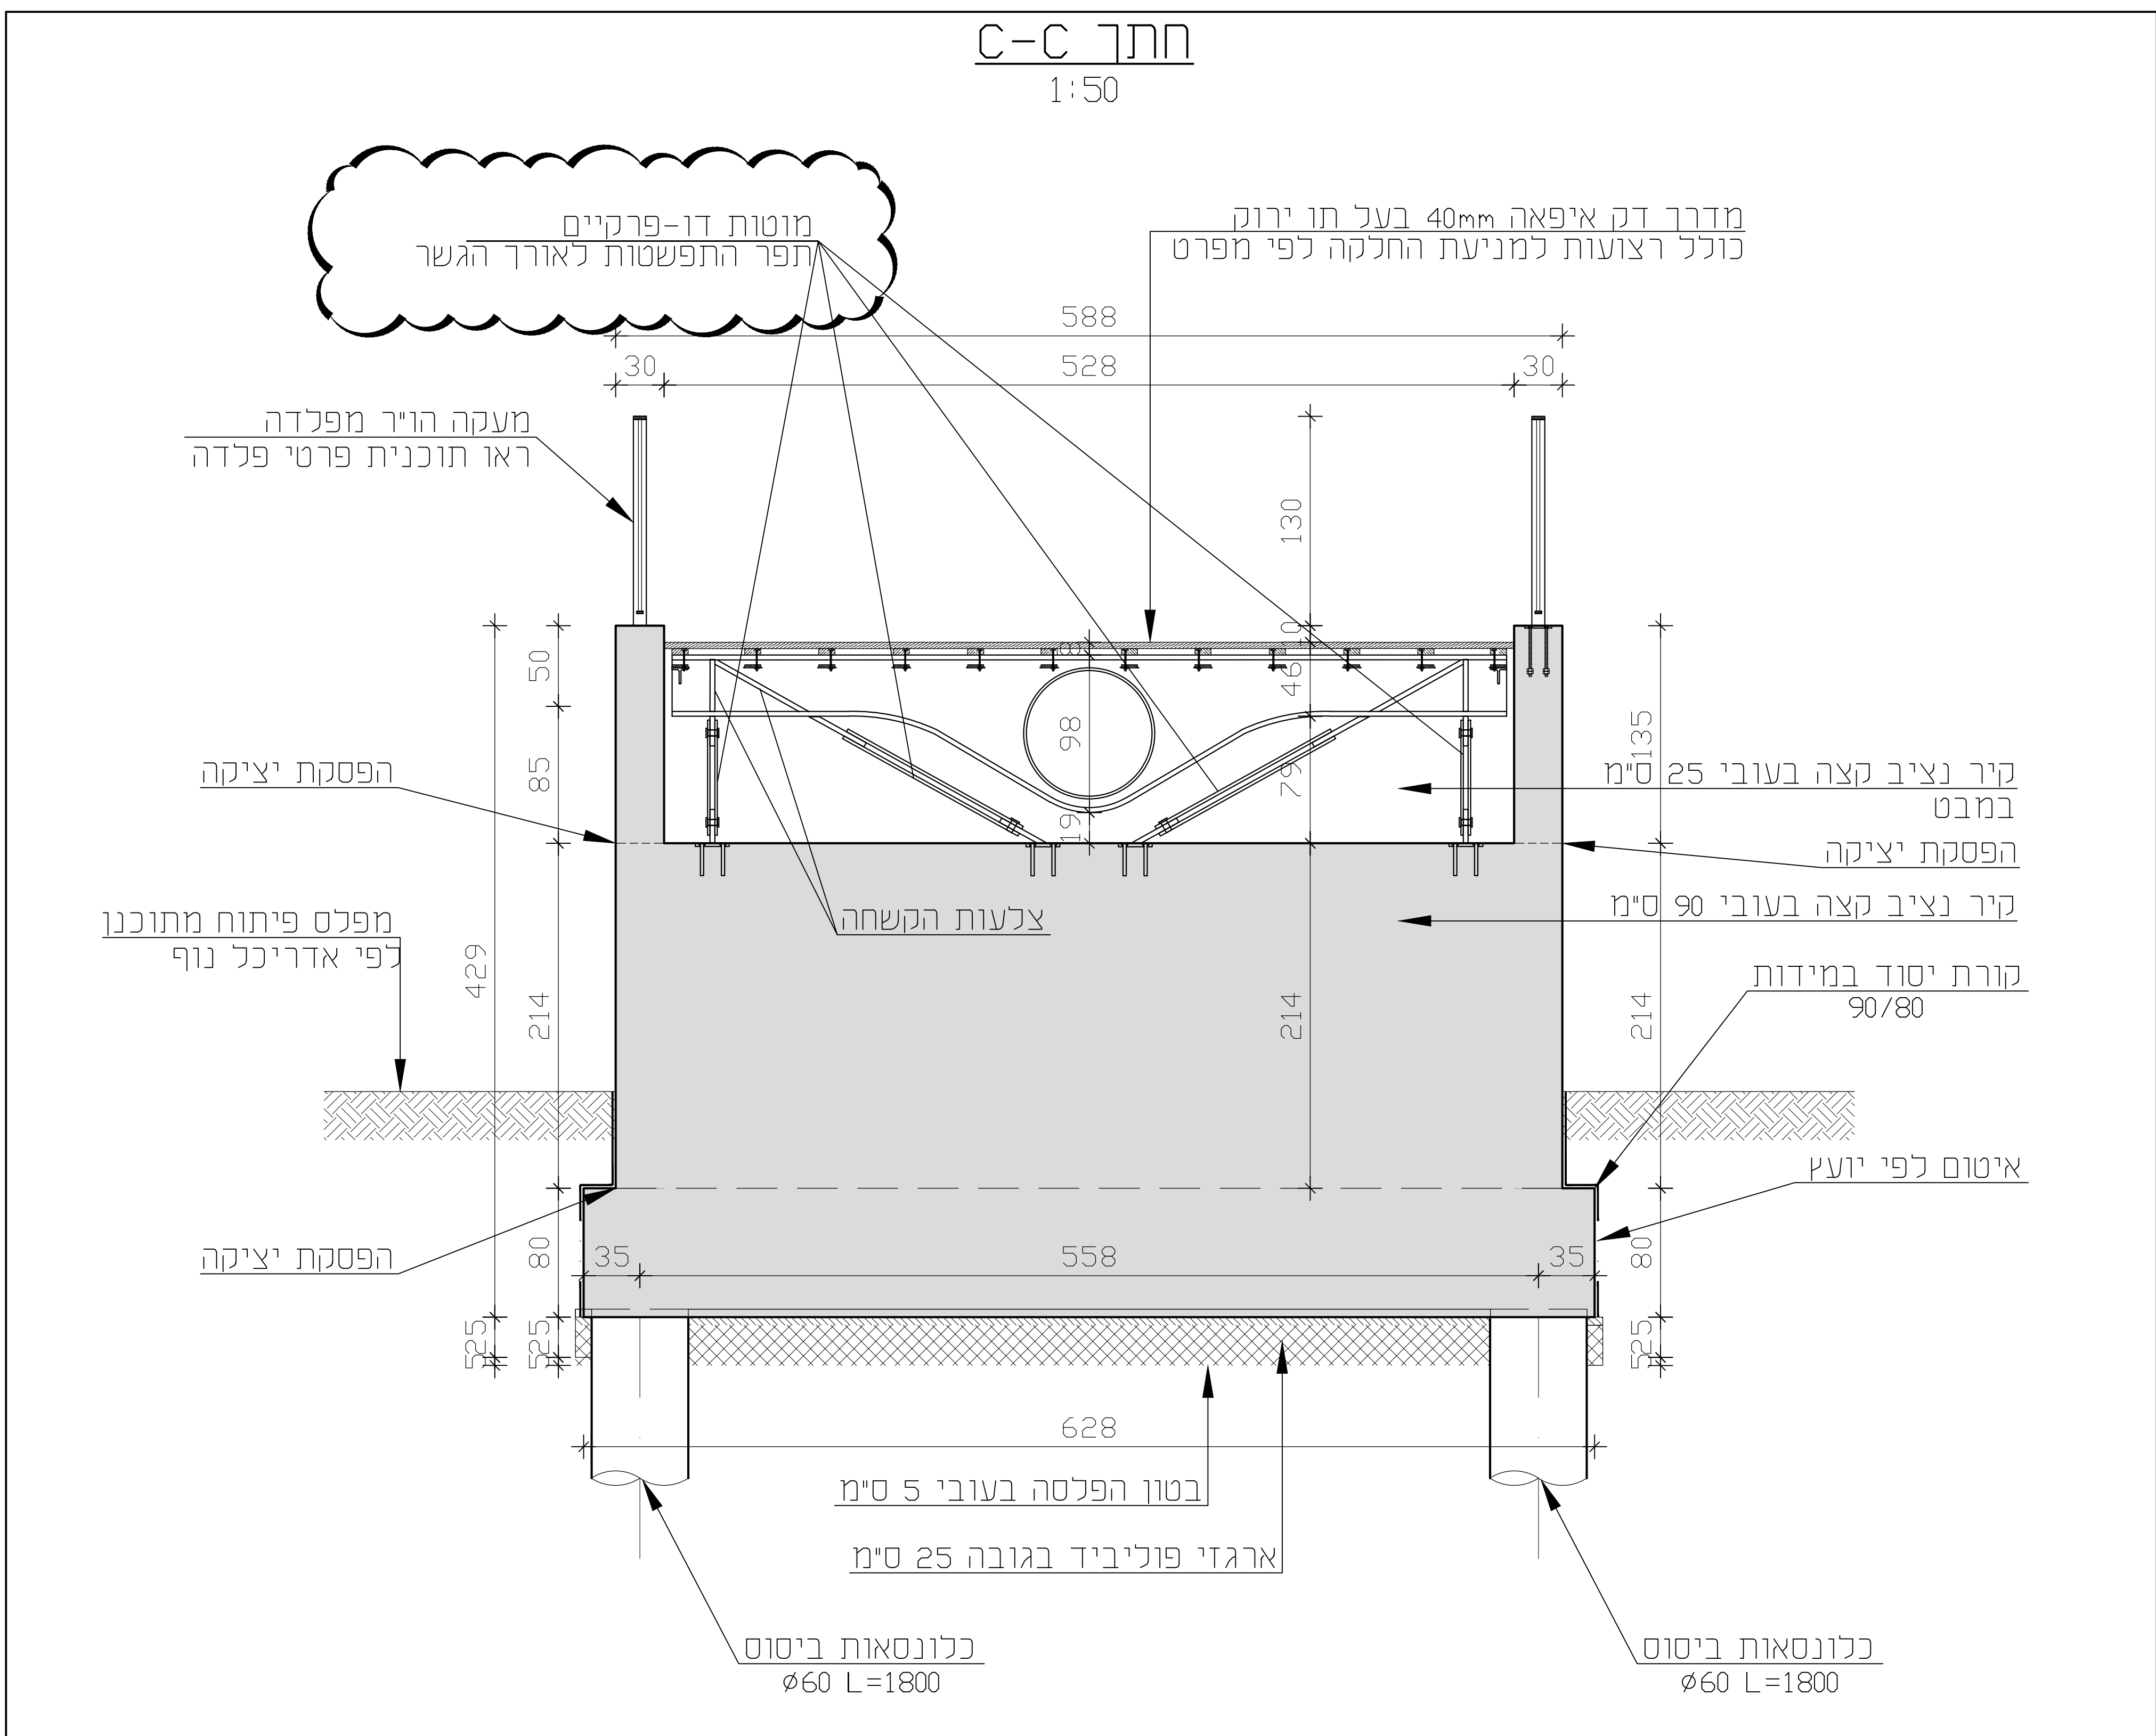
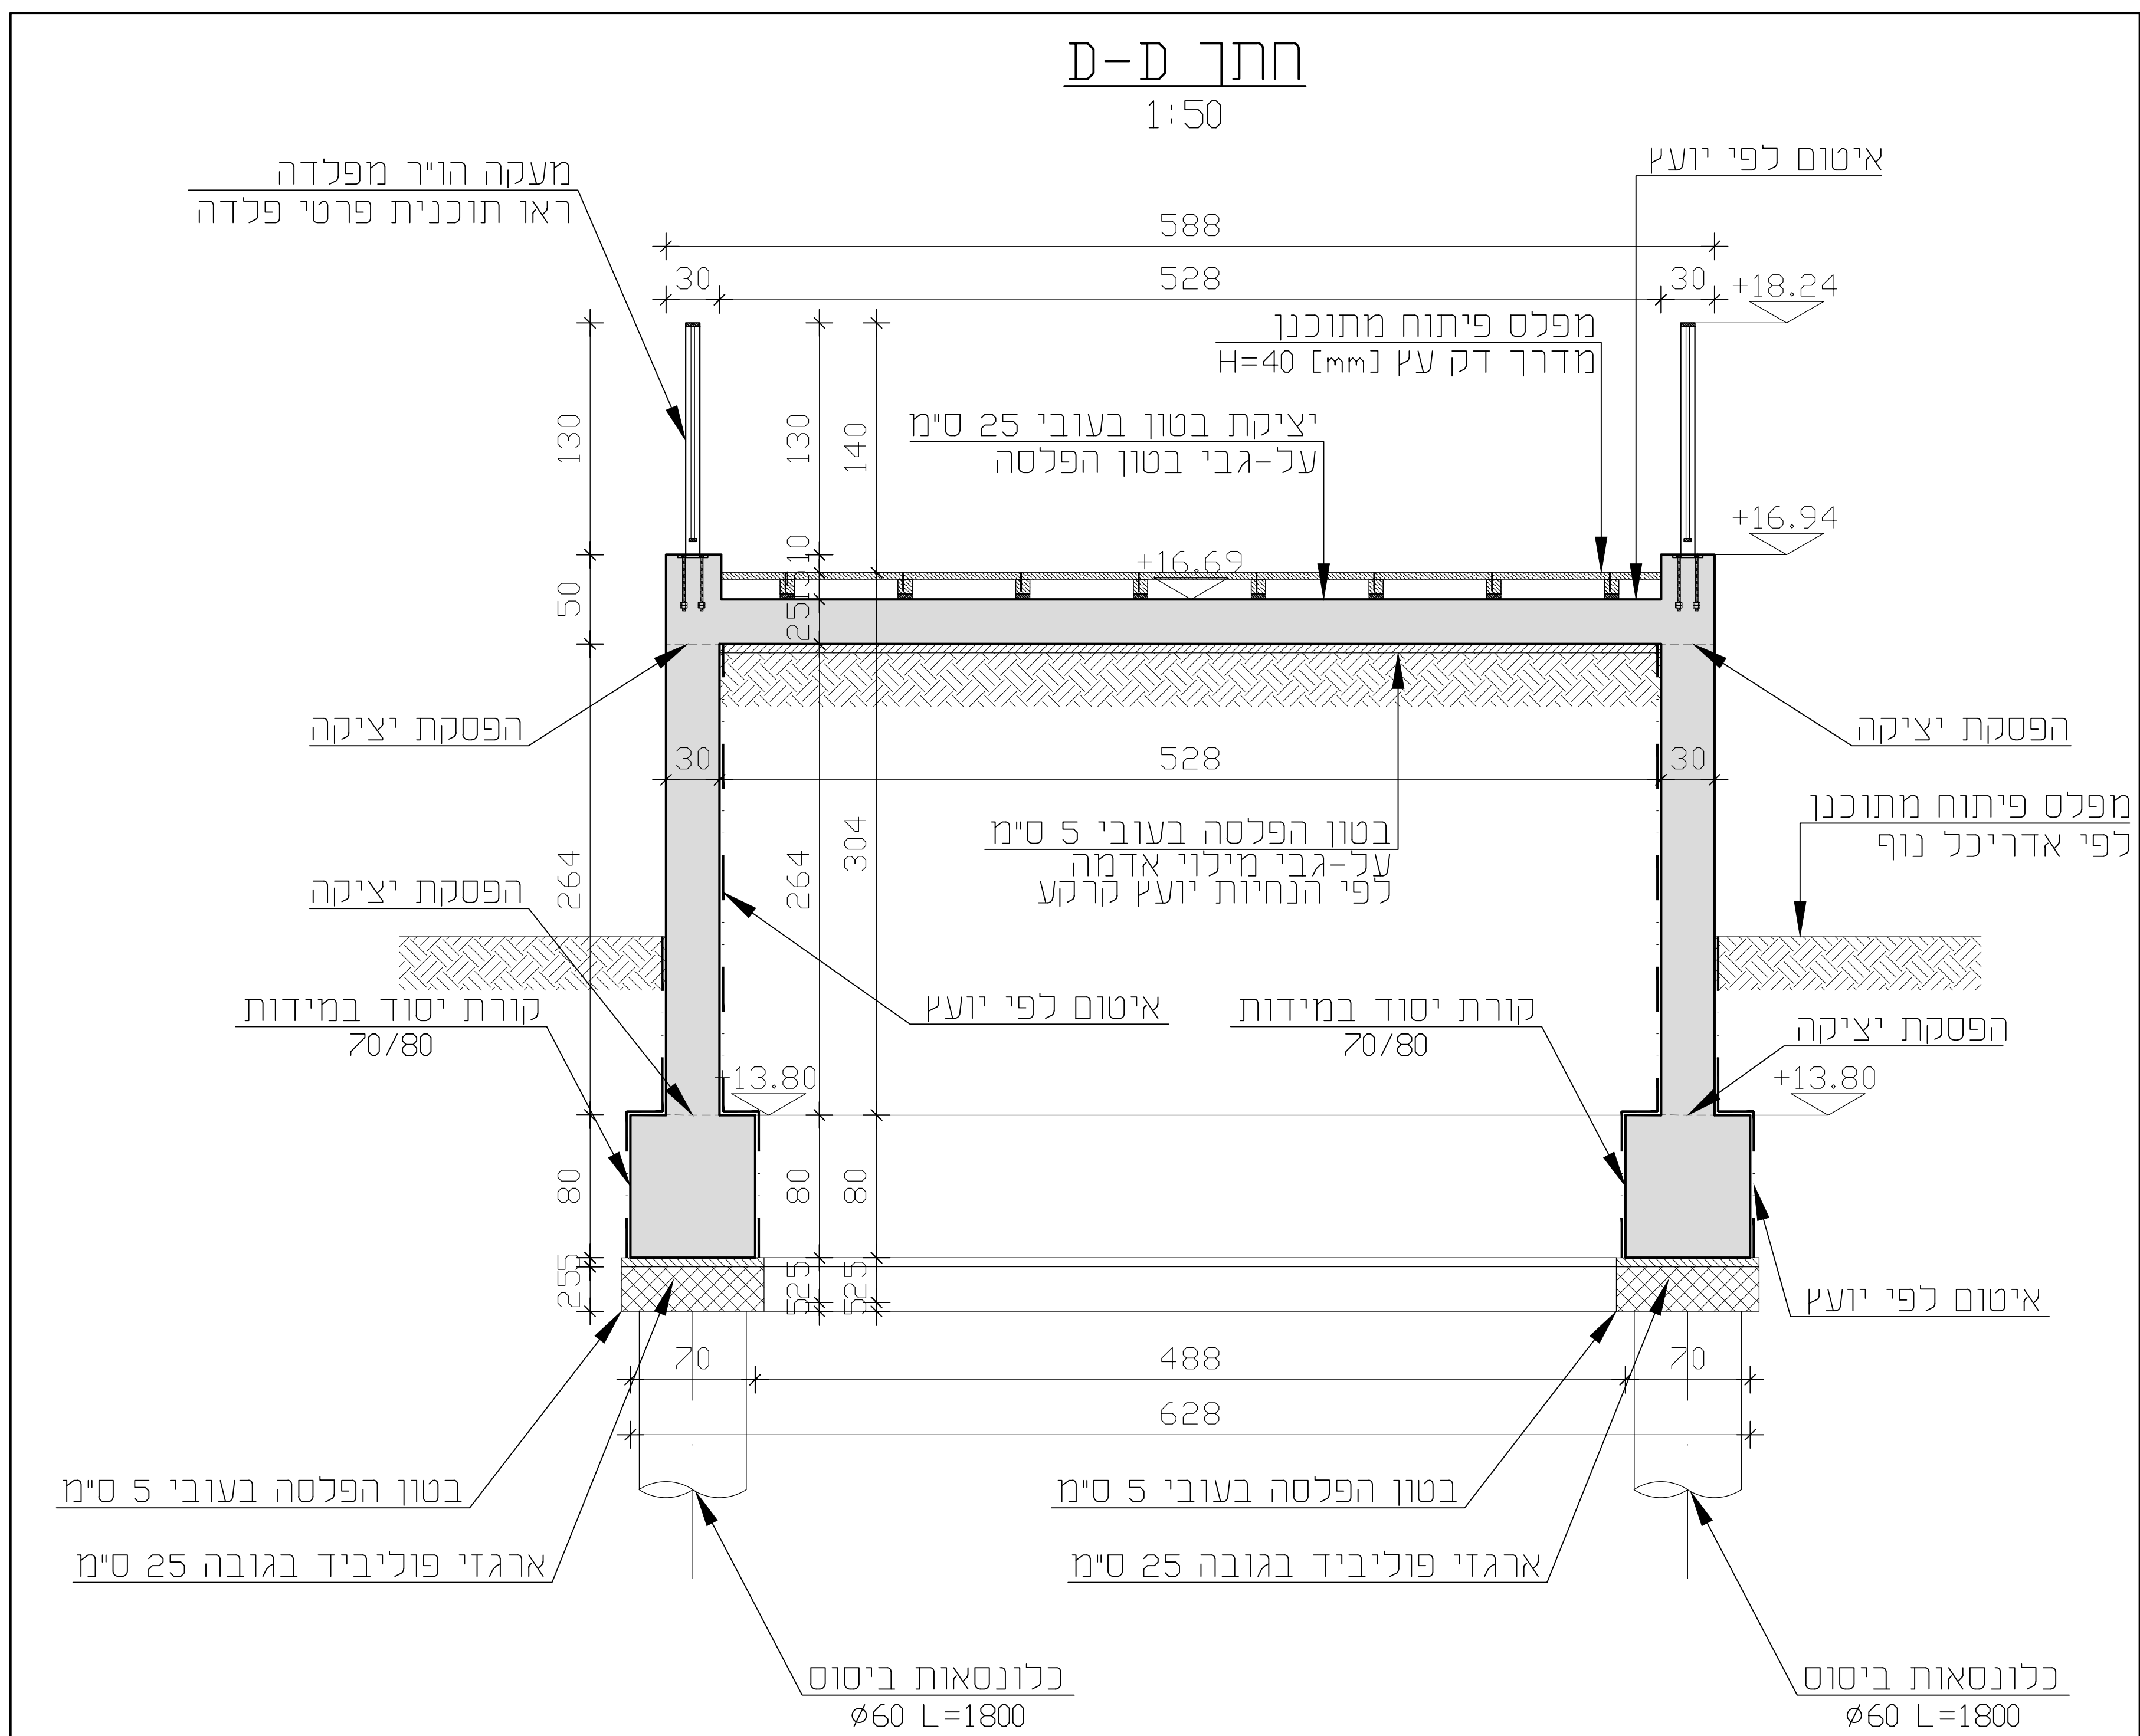



מס	תאריך	שנוי
6	00.00.00	---
5	00.00.00	---
4	00.00.00	---
3	00.00.00	---
2	00.00.00	---
1	10.11.22	עדכון פדלה, הוספת הנחיות לביצוע
0	---	---

מס'ר	ר"כ"ר	סוג כח/כוח	סוג חומר	סוג התכונה	סוג חומר	סוג חומר	סוג חומר	סוג חומר
1	נכון והפסד	30-1 CEM-II 42.5N	-	-	-	-	-	-
2	נכון/נכונות	40-1 CEM-I 52.5N	-	-	-	-	-	-
3	ראשון/נכון	40-3 CEM-II 42.5N	-	-	-	-	-	-
4	נכון/נכונות	40-3 CEM-I 52.5N	-	-	-	-	-	-
5	נכון/נכונות	40-3 CEM-II 42.5N	-	-	-	-	-	-
6	נכון/נכונות	40-3 CEM-I 52.5N	-	-	-	-	-	-

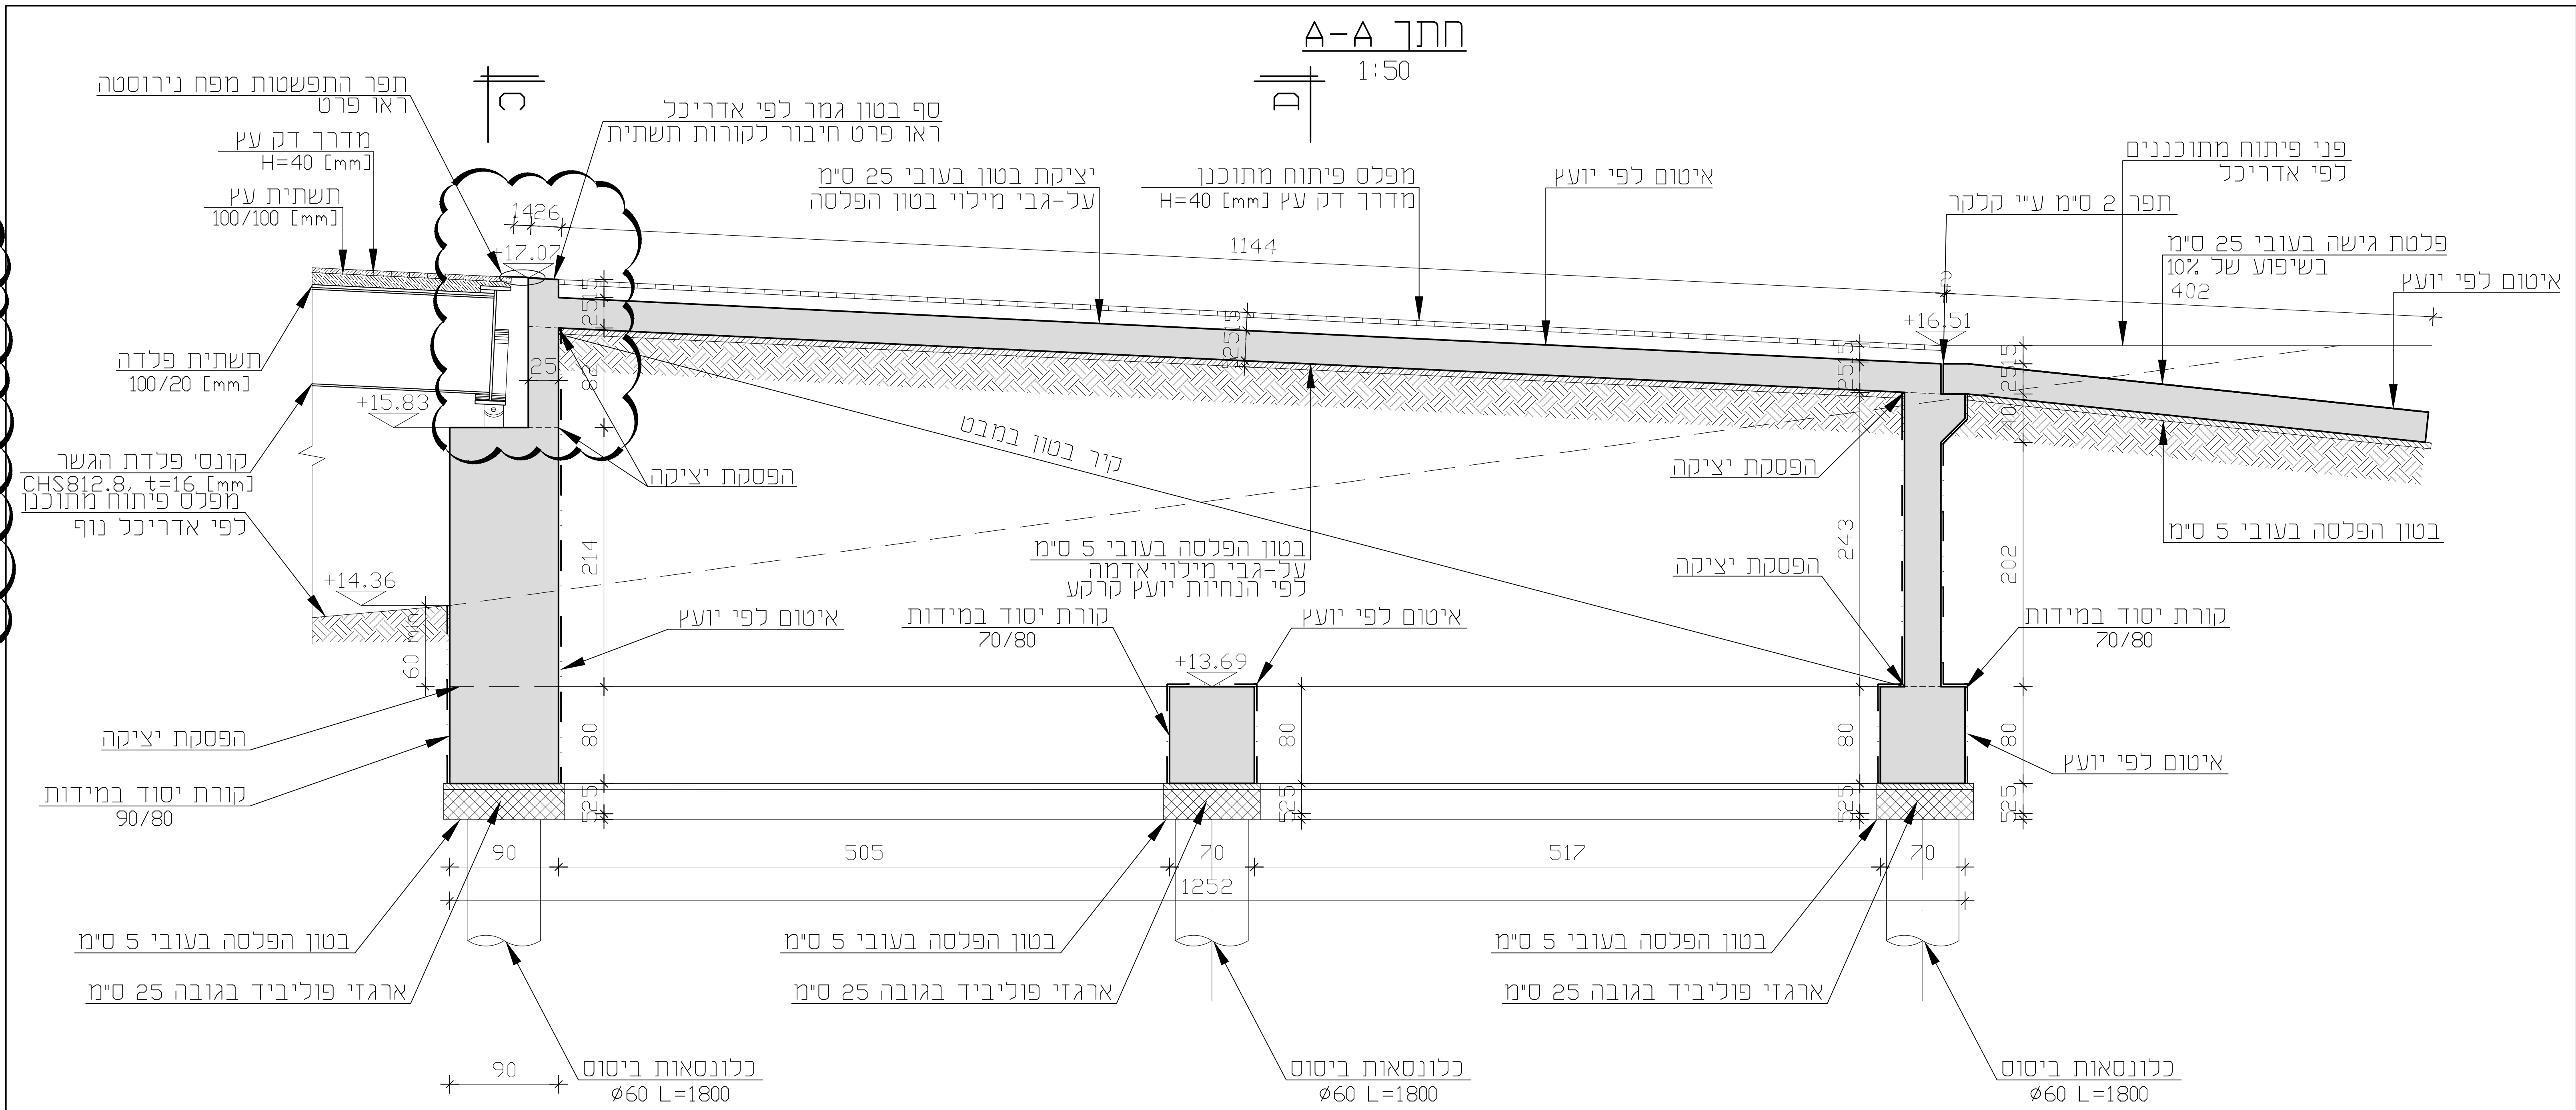

מתחם ה-1000 ג'
גשר הו"ר בפארק

חז"ל ראשון לציון			
אדריכלות			
צורנמל-טרנר			
שם החברה חזיתית רמפה מזרחית תבניות			
שם הסוכן 833.1-02-RAMPS			
מספר התכנית 833.1-04-20			
תאריך סמך 10.11.2022	שם ד"ר/בורק	שם ש. כו	חבר ש. כו
שם 01	כביש ☒	מסדר ☐	קטע/אישור ☐
תעודת 150			

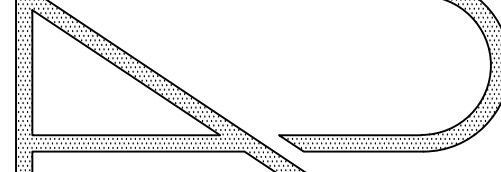
רָוֶקֶז & אֶשְׁכּוּדִי
הַתְּהַדוּסִים יְהוּעִימִים בְּעִם
רוֹד בּוֹרֶז 52 מ"מ RA-ENG-RA: E-mail
ס"ד 6994427-03 03-6995808
WWW.RA-ENG.COM