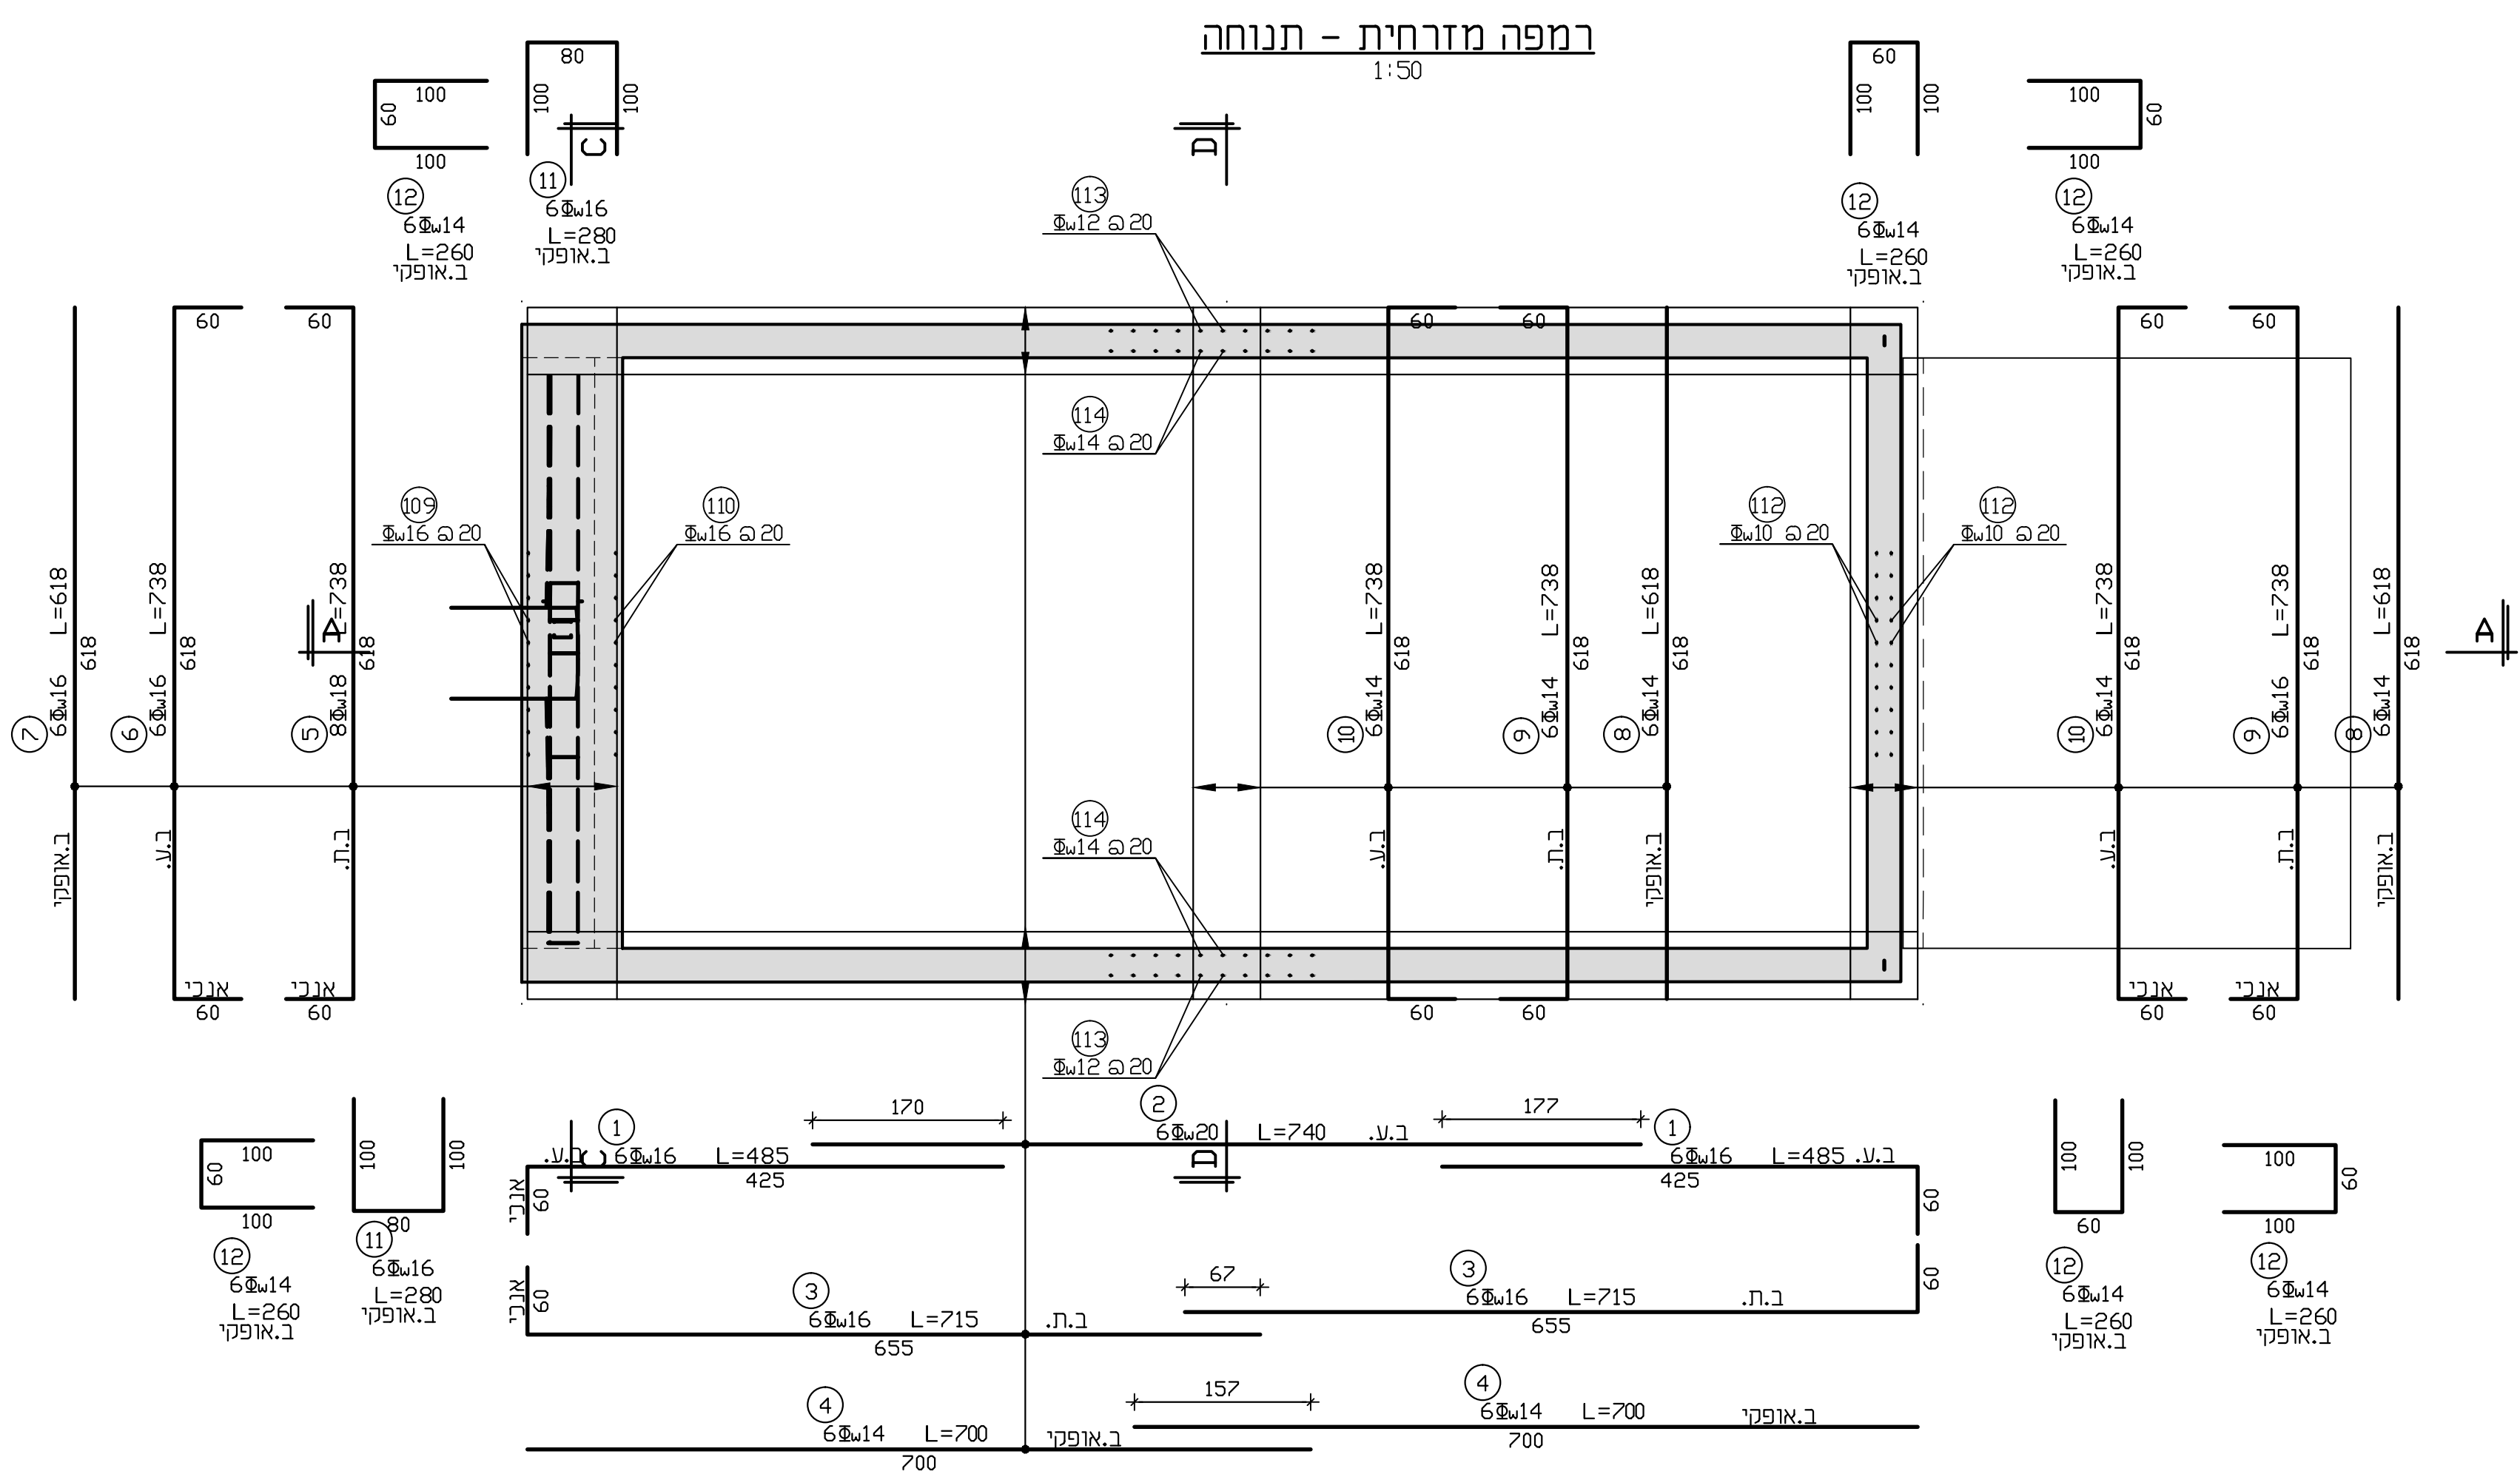
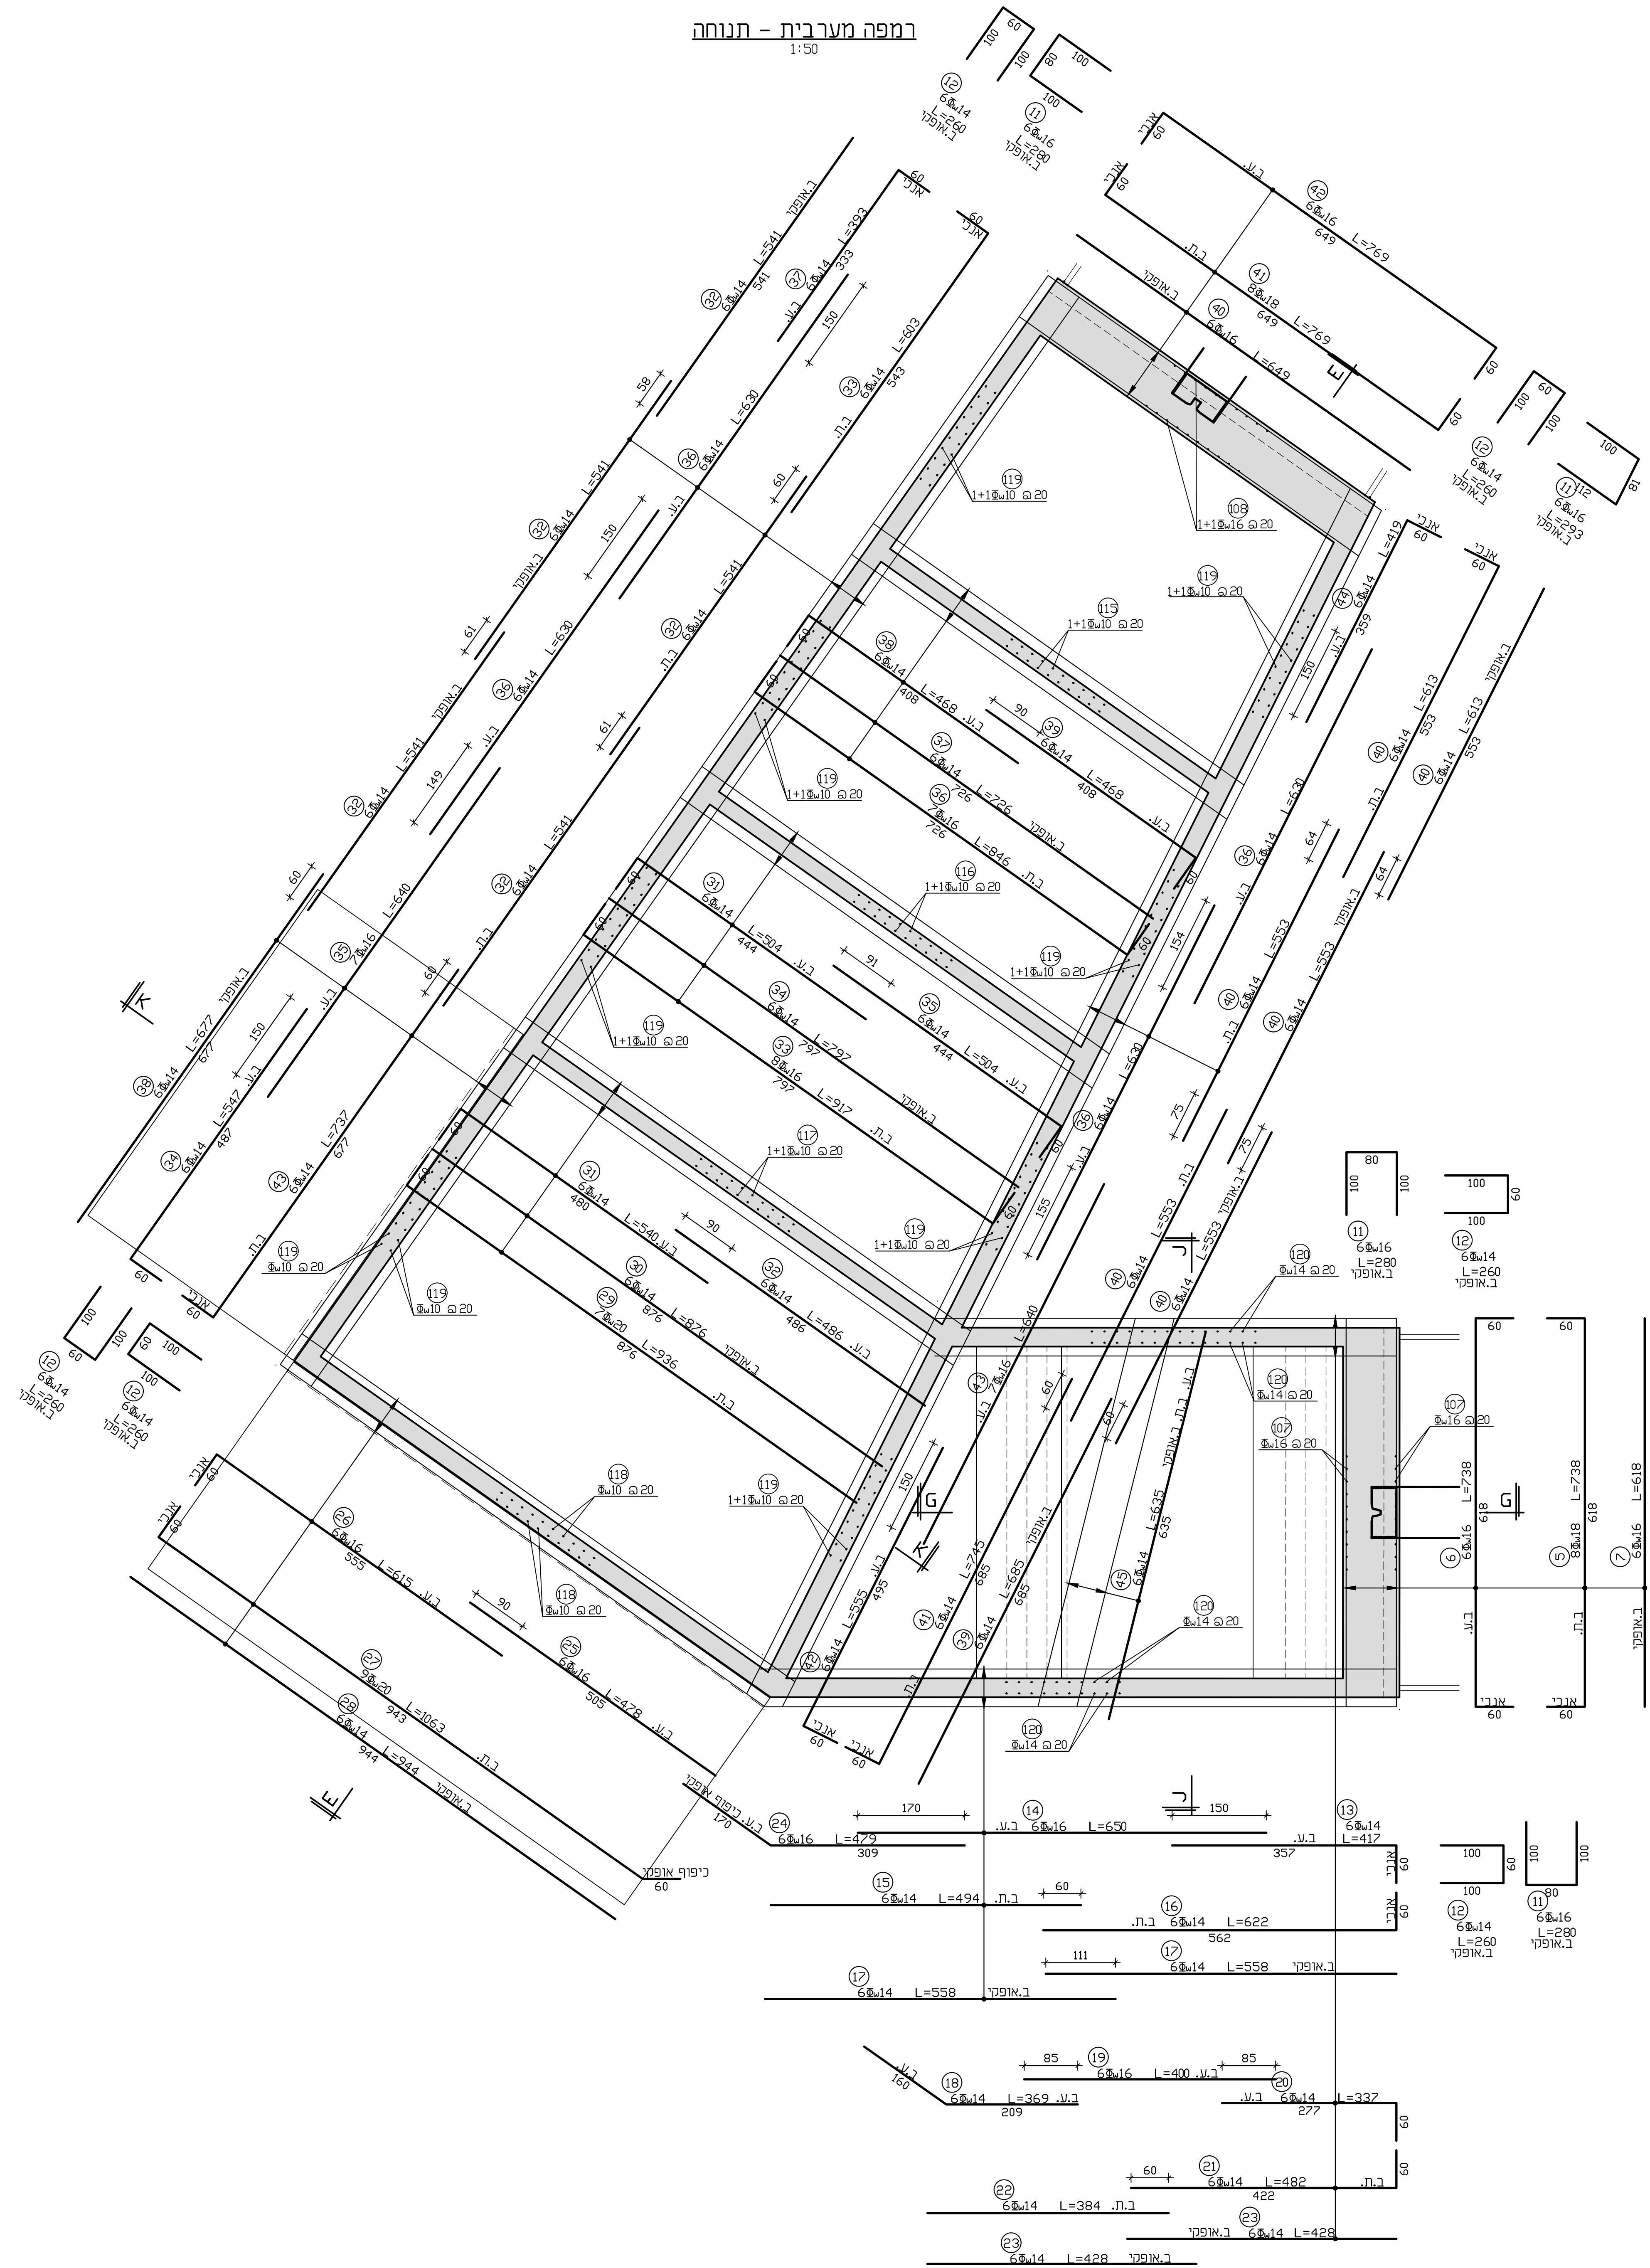


[illegible]


רוקד & אשכנזי
מחודשים יוצעים בע"מ
פ' בורלא 52 ת"א E-mail: RA@RA-ENG.COM
03-6995808 : 079 03-6994427 : 70
WWW.RA-ENG.COM

[illegible]

מתחם ה-1000 ג'
גשר הו"ר בפארק

דזכ"ל ראשון לציון

צורנמל-טערנר

תכנית קורות יסוד
ברזלים

33.1-02-20-RAMPS

833.1-05-20

תאריך	חכמה	שם
-------	------	----

לביצוע	למכרז	לעיון/לאישור
--------	-------	--------------

12

רוקח & אשכנזי

E-mail: RAERA-ENG.COM חת" 52 בורגל רת
03-6995808 : 079 03-6994427 : 70
WWW.RA-ENG.COM